

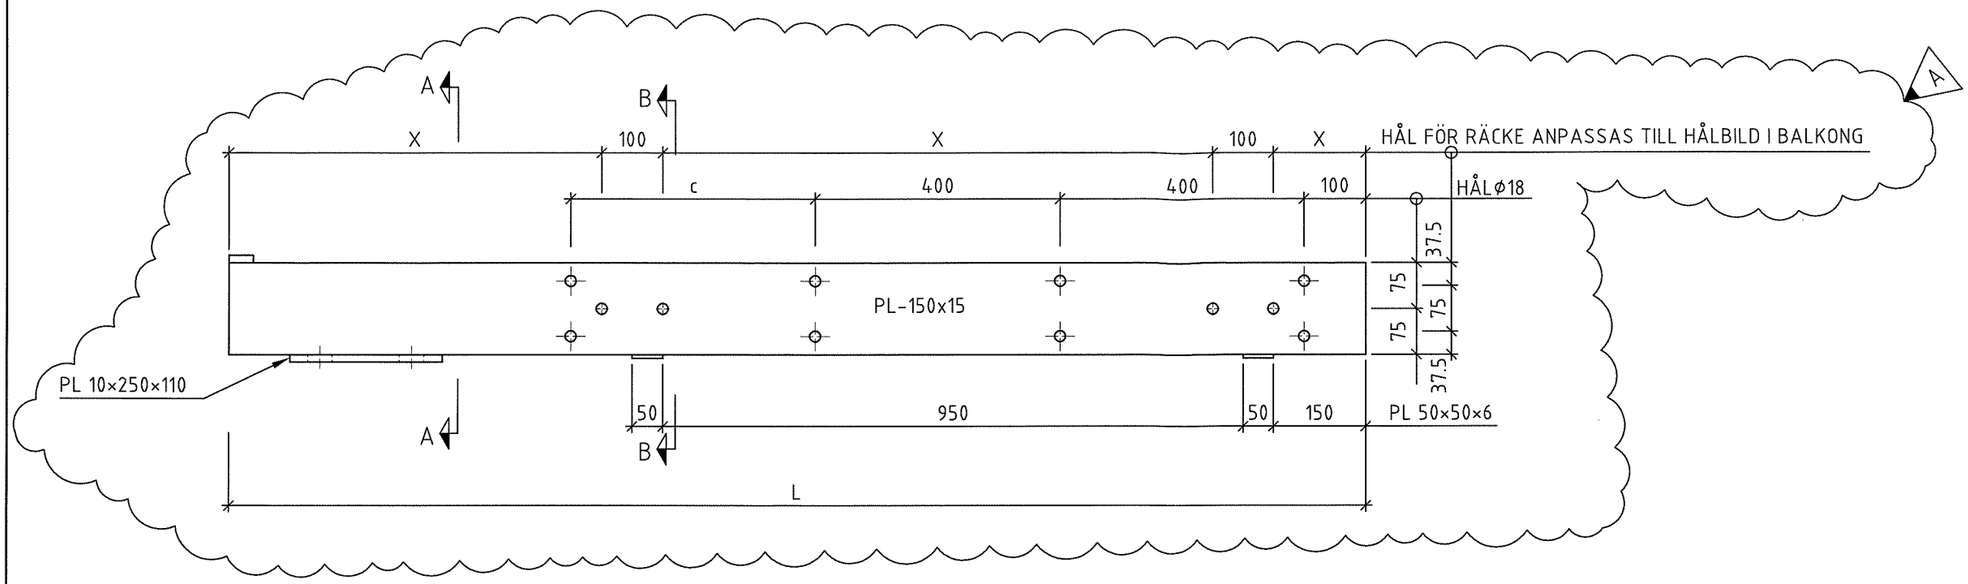



VY 1:10

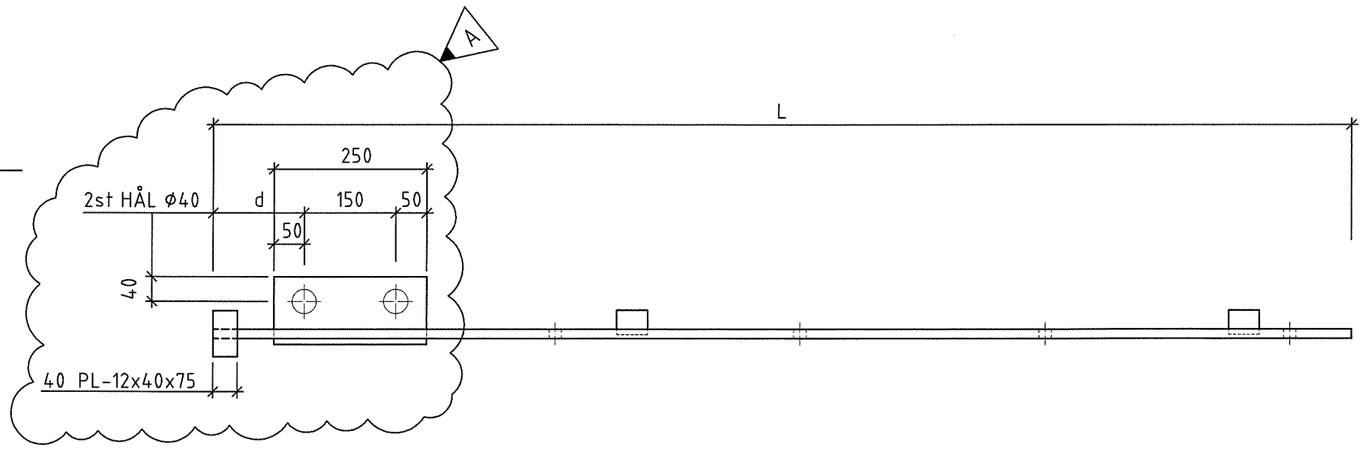

PLAN 1:10

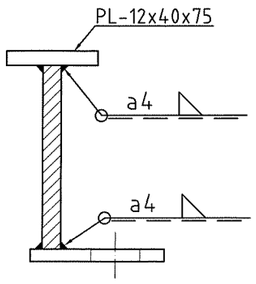

SNITT A-A 1:5

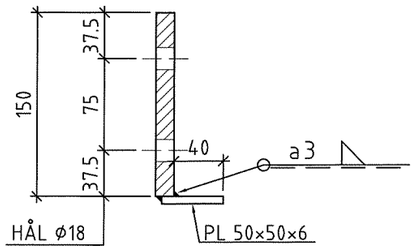

SNITT B-B 1:5

FÖRESKRIFTER

STÅL:S355J0

KORROSIVITETSKLASS C3 (VFZ 80my)

UTFÖRANDEKLASS EXC 2

VARIABLER c,d.L ENL. SAMMANSTÄLLNINGS RITNING.

BET	ANT	ÄNDRINGEN AVSER	DATUM	SIGN
A	2	NYA MÅTT	18.11.22	TS

ARBETSHANDLING

SWK
Stridsberg o Wikenstål Konstruktioner AB
Dalhemsvägen 30
141 46 Huddinge
08-689 70 00
www.swkab.se

UPPDRAG NR	RITAD/KONSTR AV	HANDLÄGGARE
	TS	TS

DATUM 2018.11.14

ANSVARIG

PREFABRICERADE LÄTT-BALKONGER
KONSOLANDE STÅLBALKAR

SKALA	HALVSKALA	NUMMER	BET
1:10:5		T-16V	A

Inkom till Stockholms stadsbyggnadskontor - 2021-08-18, Dnr 2021-07546