

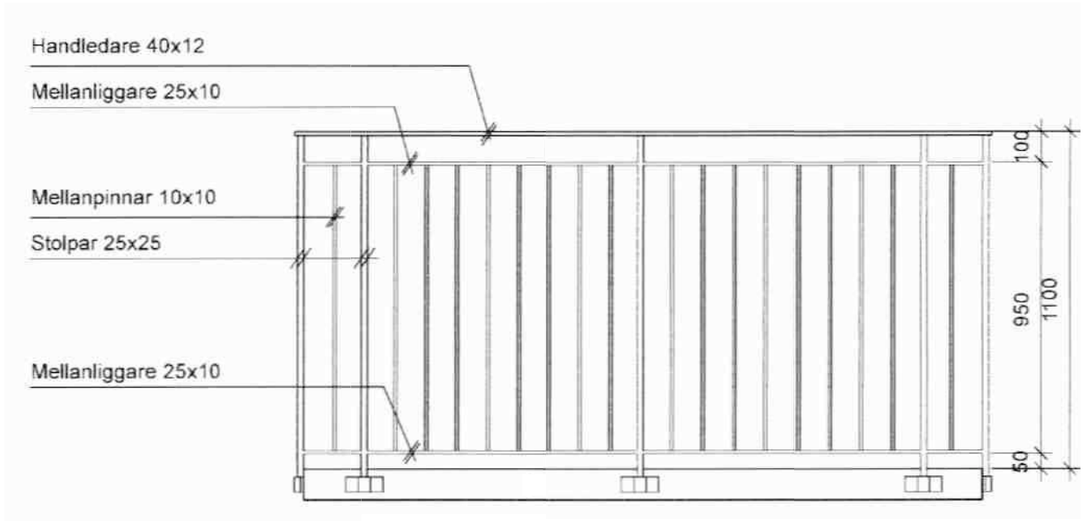


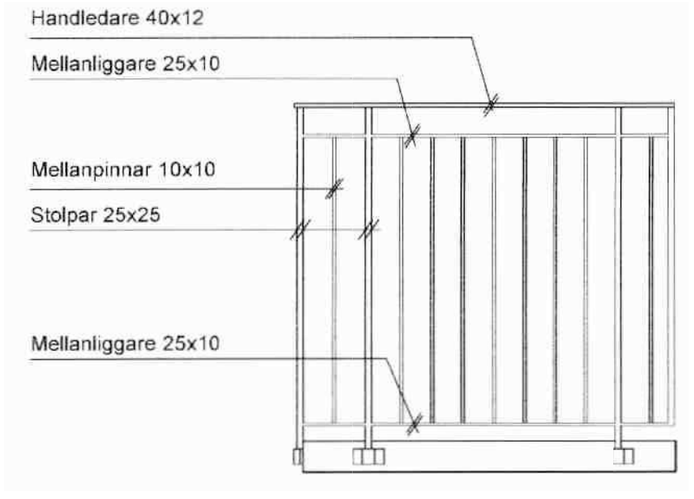


SKALA 1:20

0 0,1 0,5 1 1,5 2

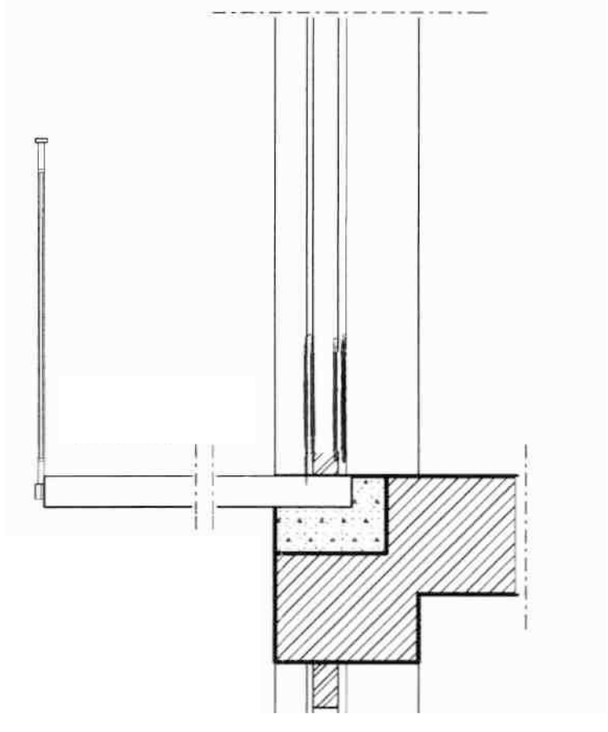

SKALA 1:50

0 1 2 5

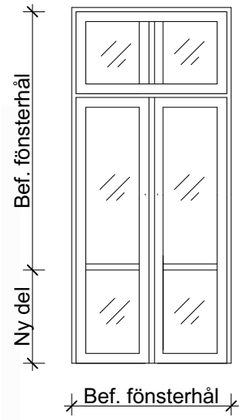

FÖRKLARINGAR OCH FÖRESKRIFTER

MÅTT I MILLIMETER.
MÅTT KONTROLLERAS PÅ PLATS.

INFORMATION

DETTA BYGGLOV KOMPLETTERAR TIDIGARE LOV
FÖR BEVILJADE BALKONGER OCH FÖNSTERDÖRRAR.

ALLA DETALJER, MATERIAL, DIMENSIONER,
INFÄSTNING (INGJUTEN STÅLBALK, EJ DRAGSTAG)
OCH MÅTT EFTERLIKNAR BEFINTLIGA.

BET	ANT	ÄNDRINGEN AVSER	SIGN	DATUM

BYGGLOVHANDLING

Vilan 16
Roslagsgatan 37, Stockholm

Fästeb AB Bygg
Box 9096
126 09 Hägersten
Tel: 08-7440007

UPPDRAG NR	RITAD AV	
0012	Per Olofsson	
DATUM	ANSVARIG	
2024 - 09 - 12	Per Olofsson	

Ny balkong
Elevation
Balkongräcke, fönsterdörr

SKALA	RITNINGSNUMMER	BET
1:20 / 1:50 (A3)	A49-1-1	

Inkom till Stockholms stadsbyggnadskontor - 2024-09-13, Dnr 2024-13805