



ORIENTERINGSFIGUR

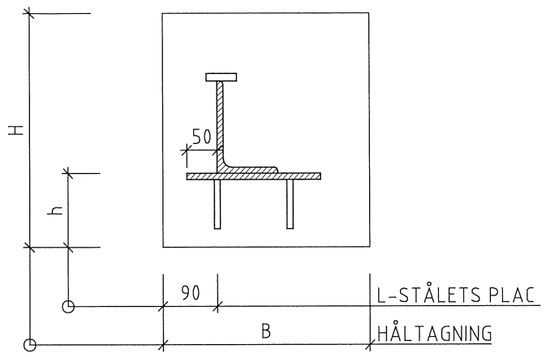


DETALJ 1 1:10

HÅLTAGNING I VÄGG.
UPPLAGSPLÅT ENL. K-11.

# FÖRESKRIFTER

## GÄLLANDE BESTÄMMELSER

BALKONGEN ÄR DIM. FÖR LAST ENL BFS 2022:4 EKS 12
SÄKERHETSKLASS 3
SS-EN 1090-2.
NÄR INGET ANNAT ANGES GÄLLER
REKOMMENDATIONERNA I SBI:s HANDBOK OM
TILLÄMPNINGAR AV EN 1090-2

## MATERIAL

### STÅL

ENL.TILLV.RITN

### BETONG


ENL. MA-5

### TEGEL

OM MURVERK UPPVISAR SPRICKOR,SKADOR
ELLER OM VÄGGEN INNEHÅLLER NÅGON FORM
AV HÅL,SCHAKT SKA KONSTRUKTÖREN
KONTAKTAS.
VID HÅLTAGNING FÖR DÖRR NÄRMRE ÄN 500mm
TILL INFÄSTNING SKA SÅGNING ELLER VARSAM
BILNING TILLÄMPAS.

### ÖVRIGT

BALKONGPLATTA OCH RÄCKE DIMENSIONERAS
AV TILLVERKAREN.
K-HANDLING GÄLLER FÖR BYGGLOVSRITNING
DAT 2024-09-12

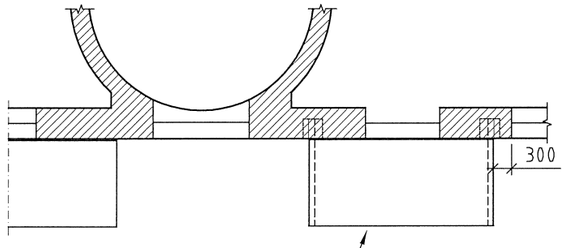


BALKONGRAD B 3000x1400
VÅN 2, VÄGGHÅL: ENL DETALJ 1 (B=340, H=380,h=130)
TILLV: T-39V,T-39H (L=1735,d=100,c=1270)
MONT: MD40, (D=300)

**OBS! BALKONGERNA MONTERAS BARA I VÅN 2**
VÅNING 4 ÄR ÖVERSTA VÅNINGEN.

| BET | ANT | ÄNDRINGEN AVSER | DATUM | SIGN |
|---|---|---|---|---|
| | | | | |
| | | | | |
| | | | | |

BYGGHANDLING

FÄSTEB BYGG AB
TOTALENTREPRENÖR FÄSTEB BYGG AB
BOX 9096, 126 09 HÄGERSTEN
TEL: 08-744 00 07
FAX: 08-744 00 08
WWW.FASTEB.SE

TSK
T STRIDSBERG KONSTRUKTIONER AB
KONSUMENTVÄGEN 8D
125 30 ÄLVSJÖ
08-689 70 00

| UPPDRAG NR | RITAD/KONSTR AV | HANDLÄGGARE |
|---|---|---|
| 2024-1088 | TS | TS |


| DATUM | ANSVARIG |
|---|---|
| 2024.10.10 | |

KV. VILAN 16. STOCKHOLM
LÄTTBALKONGER
SAMMANSTÄLLNINGSRITNING


| SKALA | HALVSKALA | NUMMER | BET |
|---|---|---|---|
| 1:100 | | K-2438 | |

## FÖRESKRIFTER


KORROSIVITETSKLASS C3 (VFZ 80my)
UTFÖRANDEKLASS EXC2
STÅL:S235
HÅL FÖR RÄCKESINFÄSTNING ENL. RÄCKES LEV.
VARIABLER c.d.L ENL. SAMMANSTÄLLNINGS RITNING.

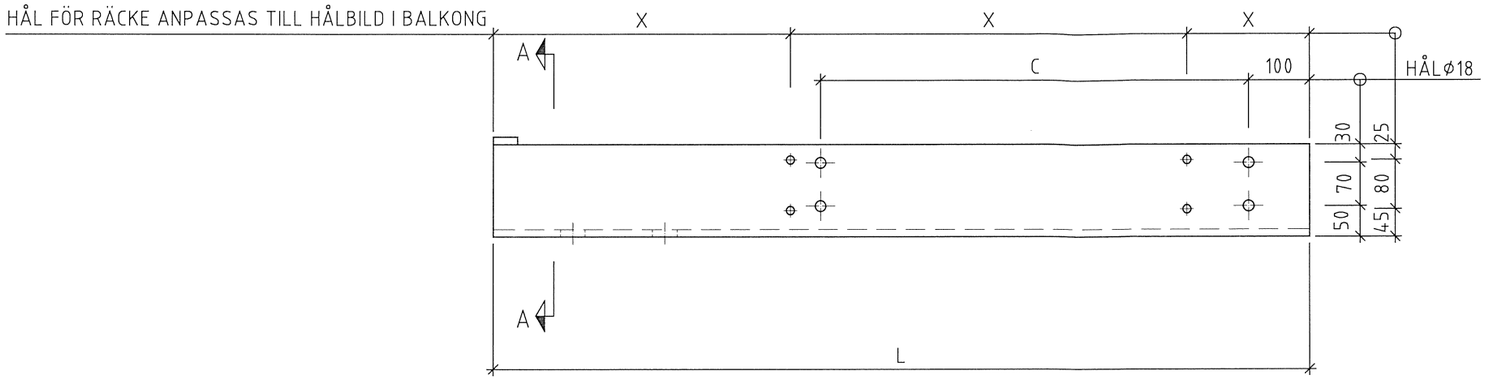


VY 1:10

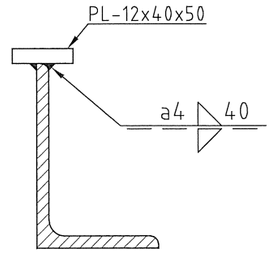


SNITT A-A 1:5

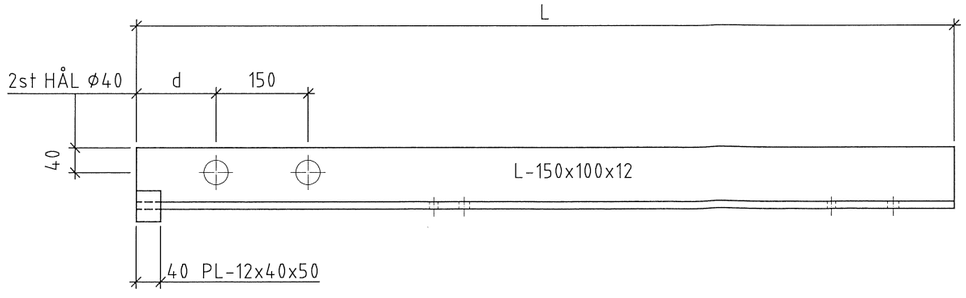


PLAN 1:10

| BET | ANT | ÄNDRINGEN AVSER | DATUM | SIGN |
|---|---|---|---|---|

BYGGHANDLING


TSK
T STRIDSBERG KONSTRUKTIONER AB
KONSUMENTVÄGEN 8D
125 30 ÄLVSJÖ
08-689 70 00


| UPPDRAG NR | RITAD/KONSTR AV | HANDLÄGGARE |
|---|---|---|
| | TS | TS |


DATUM 2024.10.10
ANSVARIG

LÄTTBALKONGER
KONSOLANDE STÅLBALKAR


| SKALA HALVSKALA | NUMMER | BET |
|---|---|---|
| 1:10:5 | T-39V | |

## FÖRESKRIFTER


KORROSIVITETSKLASS C3 (VFZ 80my)
UTFÖRANDEKLASS EXC2
STÅL:S235
HÅL FÖR RÄCKESINFÄSTNING ENL. RÄCKES LEV.
VARIABLER c.d.L ENL. SAMMANSTÄLLNINGS RITNING.

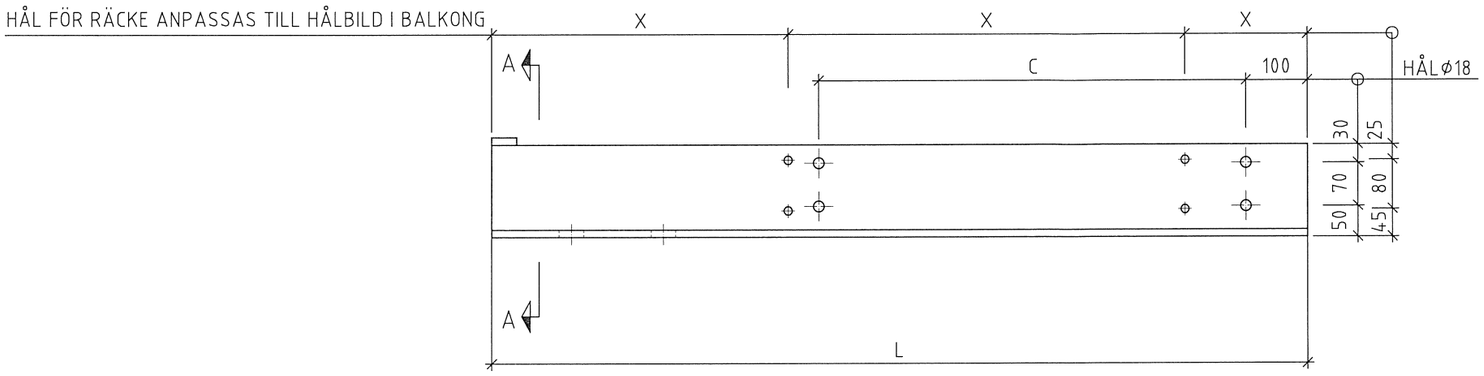


VY 1:10

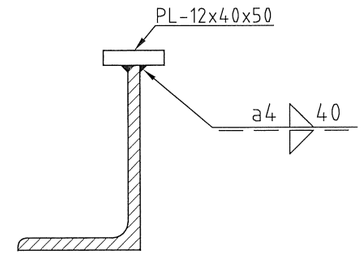


SNITT A-A 1:5

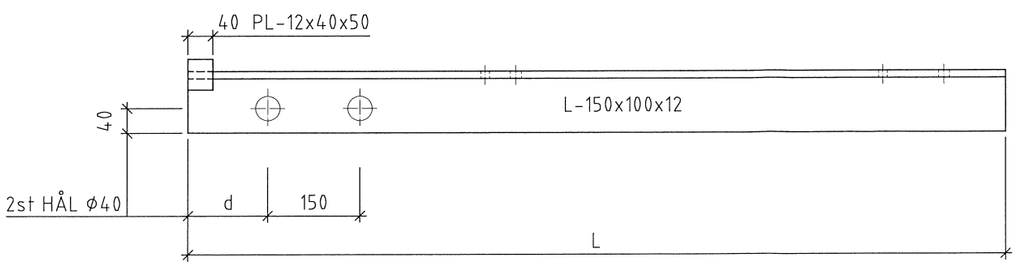


PLAN 1:10

| BET | ANT | ÄNDRINGEN AVSER | DATUM | SIGN |
|---|---|---|---|---|

BYGGHANDLING


T STRIDSBERG KONSTRUKTIONER AB
KONSUMENTVÄGEN 8D
125 30 ÄLVSJÖ
08-689 70 00



| UPPDRAG NR | RITAD/KONSTR AV | HANDLÄGGARE |
|---|---|---|
| | TS | TS |
| DATUM | ANSVARIG | |
| 2024.10.10 | | |

LÄTTBALKONGER
KONSOLANDE STÅLBALKAR


| SKALA | HALVSKALA | NUMMER | BET |
|---|---|---|---|
| 1:10:5 | | T-39H | |

## MONTERINGSANVISNING


SE RITNING MA-5
VARIABLER B,D,H,h,L,t ENL. SAMMANSTÄLLNINGS RITNING.

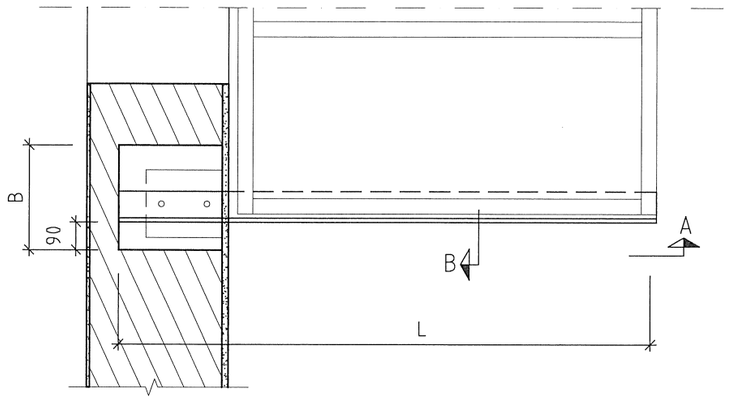


PLAN 1:20

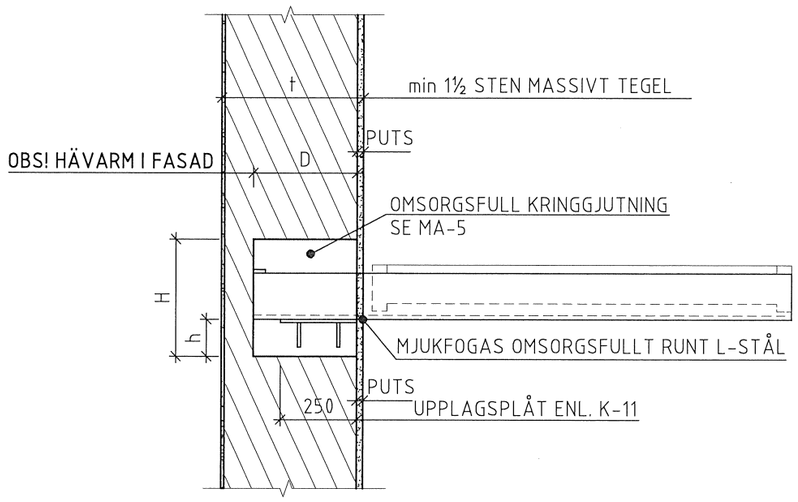


SEKTION A-A 1:20

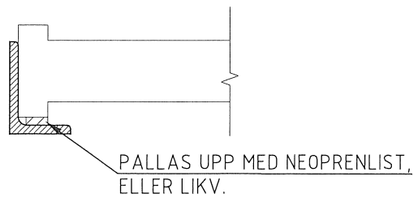


SNITT B-B 1:10

| BET | ANT | ÄNDRINGEN AVSER | DATUM | SIGN |
|---|---|---|---|---|

BYGGHANDLING


T STRIDSBERG KONSTRUKTIONER AB
KONSUMENTVÄGEN 8D
125 30 ÄLVSJÖ
08-689 70 00

| UPPDRAG NR | RITAD/KONSTR AV | HANDLÄGGARE |
|---|---|---|
| | TS | TS |


DATUM: 2024.03.26
ANSVARIG:

LÄTTBALKONG 150-160
MONTERINGS DETALJER

| SKALA / HALVSKALA | NUMMER | BET |
|---|---|---|
| 1:20:10 | MD-40 | |

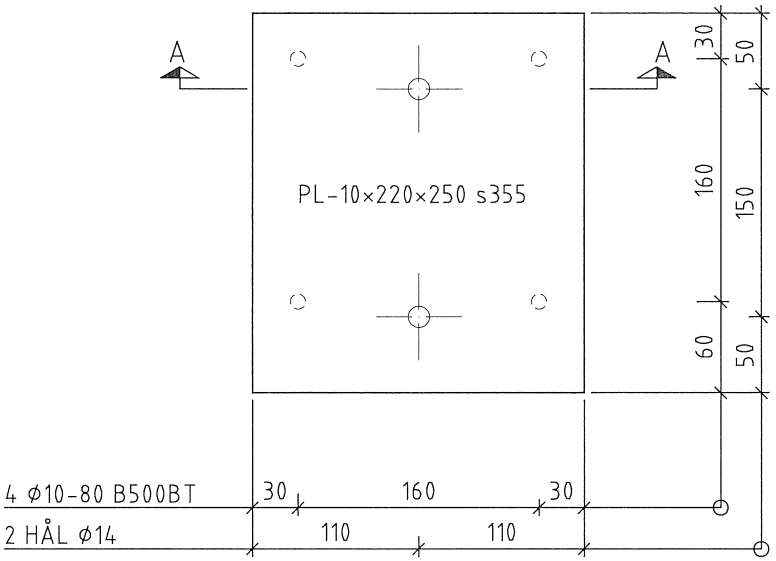


PLAN 1:5

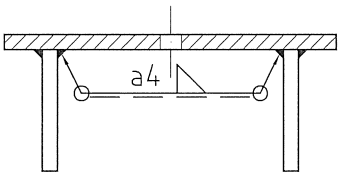


SNITT A-A 1:5

## FÖRESKRIFTER

UTFÖRANDEKLASS EXC 2
KORROSIVITETSKLASS C3 (VFZ 80my)

| BET | ANT | ÄNDRINGEN AVSER | DATUM | SIGN |
|---|---|---|---|---|
| | | | | |

T STRIDSBERG KONSTRUKTIONER AB
KONSUMENTVÄGEN 8D
125 30 ÄLVSJÖ
08-689 70 00

# BYGGHANDLING

# PREFABRICERAD LÄTTBALKONG
## UPPLAGSDETALJ

| RITAD AV | HANDLÄGGARE | ARBETSNUMMER |
|---|---|---|
| TS | TS | |

| DATUM/UNDERSKRIFT | SKALA | HALVSKALA | NUMMER | BET |
|---|---|---|---|---|
| 2023.05.23 | 1:5 | | K-11 | |

## MONTAGEANVISNING

TILL DETTA DOKUMENT HÖR ÄVEN MONTAGERITNING FÖR L-STÅL

- HÅLTAGNING FÅR EJ UTFÖRAS UNDER FÖNSTER- DÖRRÖPPNING ELLER LIKNANDE.
- OM EJ ANNAT ANGES PÅ SAMMANSTÄLLNINGSRITNINGEN FÅR INTE L-STÅLETS VERTIKALA SKÄNKEL KOMMA NÄRMARE ÄN 400mm FRÅN FRIKANT EL. DÖRRÖPPNING OCH KONSTRUKTÖREN SKA MEDDELAS.
- MIN HÅLTAGNINGSMÅTT = (B×H) SE SAMMANSTÄLLNINGSRITNING.
- HÅLTAGNINGENS INSIDA TÄTAS SÅ ATT INTE LÄCKAGE UPPSTÅR VID GJUTNING.
- HÅLET SKA UTFORMAS SÅ ATT LYFTNING AV UNDERGJUTNING FÖRHINDRAS UNDER MONTAGE AV L-STÅL, INNAN ÖVERGJUTNINGEN ÄR PÅ PLATS
- UPPLAGSPLÅT MONTERAS: I DJUPLED: I LIV MED TEGLETS UTSIDA.
  I SIDLED: 50mm UTANFÖR L-STÅLETS VERTIKALA SKÄNKEL.
  I HÖJDLED: ENL. BESLUT PÅ ARBETSPLATSEN. DOCK MIN. 120mm ÖVER UK. HÅL.
- FORM MONTERAS MOT TEGEL FÖR ATT MÖJLIGGÖRA PUTSNING UTANPÅ GJUTNING.
- UPPLAGSPLÅTEN UNDERGJUTES/ STOPPAS MED EXPANDERBETONG GROV MIN C32/40 ALTERNATIVT FINJA GROVBETONG C32/40 EL. LIKV.
  FÖR FULLGOD VIDHÄFTNING SKA TEGLET RENGÖRAS OMSORGSFULLT OCH FÖRBLÖTAS I GOD TID INNAN GJUTNING. TEGLET SKA VARA FUKTIGT MEN YT-TORRT.
  VINTERTID SKA FRYSRISKEN BEAKTAS.
- L-STÅL MONTERAS ENL MONTAGERITNING (MD-RITNING)
- L-STÅLEN JUSTERAS GENOM SKIMSNING I YTTERKANTER PÅ UPPLAGSPLÅT.
- L-STÅLEN FIXERAS TILL UPPLAGSPLÅT MED TILLHÖRANDE FIXERINGSSKRUV.
- L-STÅLEN SKA MONTERAS MED EN LUTNING MIN 1/100 (10mm/m) UT FRÅN FASADEN.
- HÅLET FORMAS OCH TÄTAS VID GJUTNING.
- LÄGESKONTROLL OCH KRYSSMÄTNING AV L-STÅLENS PLACERING UTFÖRS INNAN ÖVERGJUTNING.
- ÖVERGJUTNINGEN GJUTES/ STOPPAS MED BEMIX STD. EXPANDERBRUK ALT. FINJA GROVBETONG C32/40 EL. LIKV.

- PLATTAN FÅR INTE MONTERAS FÖRRÄN IGJUTNINGENS HÅLLFASTHETSTILLVÄXT UPPNÅTT C16
- BALKONGPLATTAN LYFTS PÅ PLATS ENL. ENTREPRENÖR.
- SKRUVAR MONTERAS MEN FÅR EJ DRAS ÅT INNAN BRICKA MELLAN L-STÅL OCH BALKONGPLATTA HAR MONTERATS.

| BET | ANT | ÄNDRINGEN AVSER | DATUM | SIGN |
|---|---|---|---|---|
| | | | | |

TSK
T STRIDSBERG KONSTRUKTIONER AB
KONSUMENTVÄGEN 8D
125 30 ÄLVSJÖ
08-689 70 00

ARBETSHANDLING

LÄTTBALKONG

MONTAGEANVISNING

| RITAD AV | HANDLÄGGARE | ARBETSNUMMER |
|---|---|---|
| TS | TS | |

| DATUM/UNDERSKRIFT | SKALA | HALVSKALA | NUMMER | BET |
|---|---|---|---|---|
| 2024.03.26 | 1:20 | | MA-5 | |

Inkom till Stockholms stadsbyggnadskontor - 2024-10-29, Dnr 2024-13805