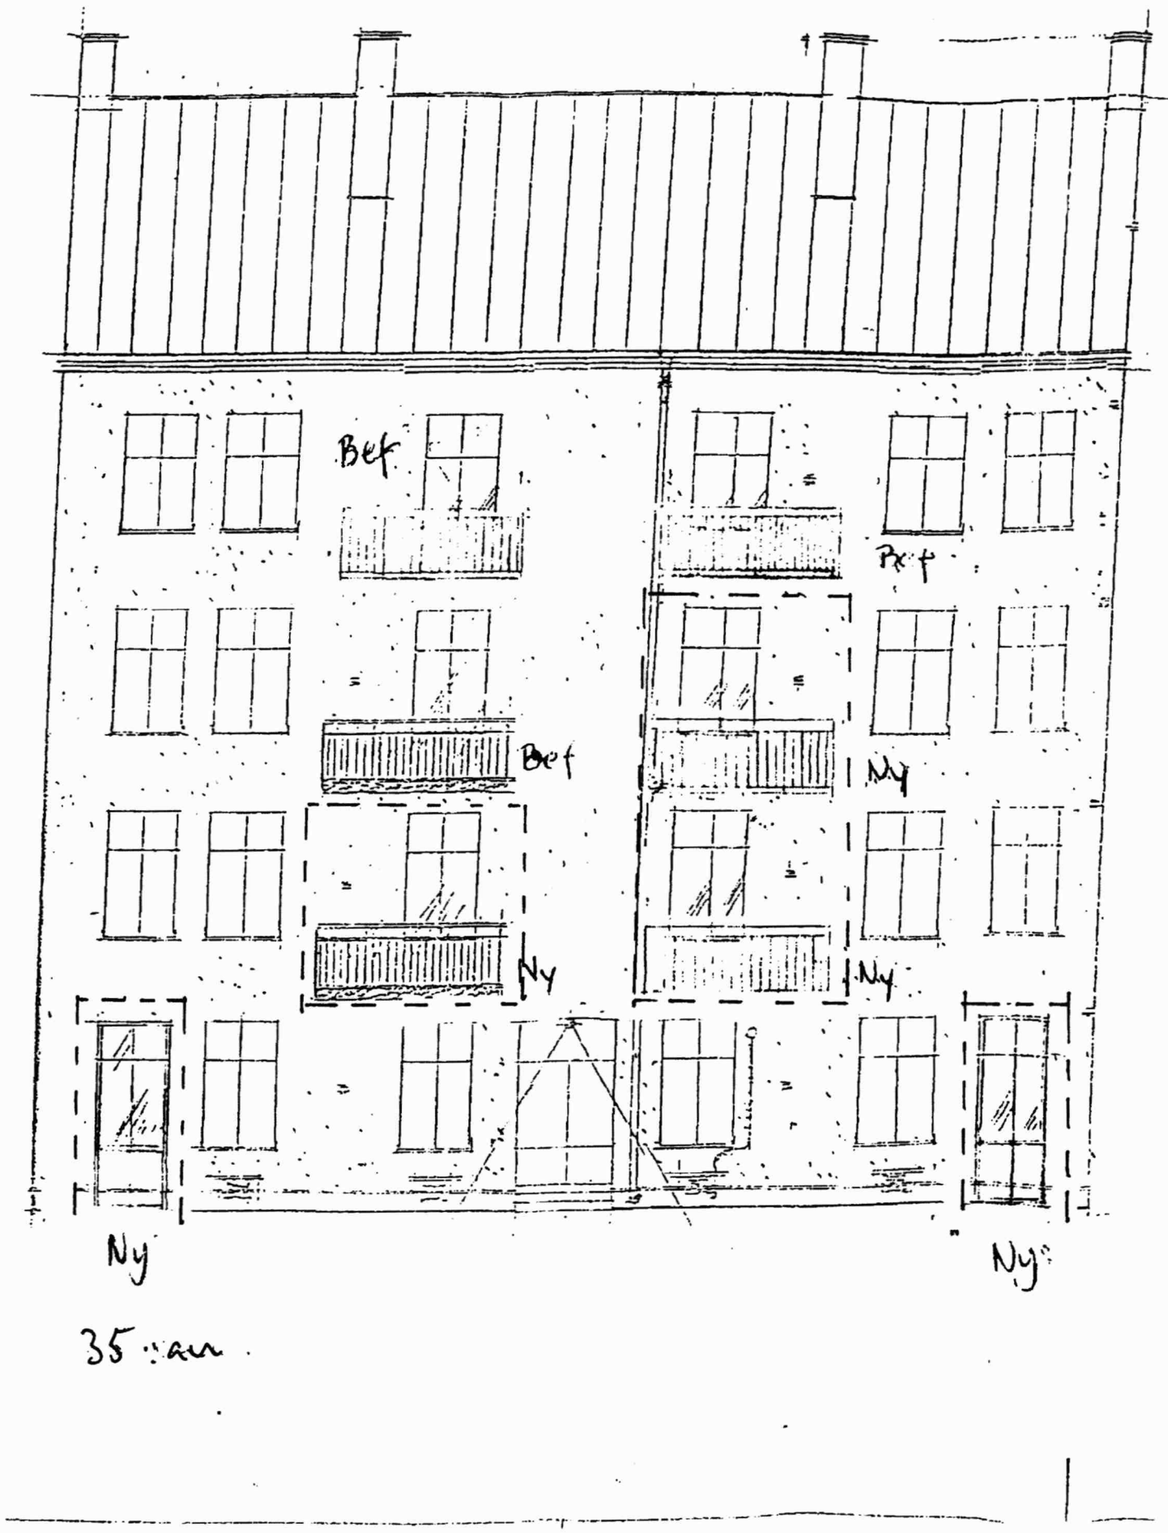



Ritning för förnyande av lov 1

35 :sam

DÅLIG FÖRLAGA

BYGGLOVSHANDLING
Kv Vilan 17
Roslagsgatan 35
Balkongplatta av betong monteras på konsoler av L-stål, ingjutna i tegelvägg.
Svarta smidesräcken.
Nya fönsterdörrar av trä lika bef. fönster
Kulör lika bef. fönster.

Altandörrar i bottenvåning

Stadsbyggnadskontoret
Inkom Reg. 2016 -10- 13
Dnr: 17088/575


Granskad STOCKHOLMS BYGGNADSNÄMND
Tillhör nämndens beslut
2009 -12- 16

Stadsbyggnadskontoret
Inkom 2009 -12- 09
Reg.
Dnr: 9-22338-57

SKALA 1:50

| | |
|---|---|
| GTL KVALITETSANSVARIG ARKITEKT | |
| ADRESS | JÄRNEKSVÄGEN 4, 131 40 NACKA |
| TELEFON | 08 - 556 152 53 |
| MOBIL | 070 - 725 23 53 |
| TELEFAX | 08 - 556 152 54 |
| UPPDRAGSANSVARIG | DATUM |
| GEORGE LEDDER | 2001-08-31 |
| BYGGLOVSHANDLING | |
| Kvarteret Vilan 17, Vasastaden | |
| ÄNDRING AV GÅRDSFASADER MED BALKONGER & FÖNSTERDÖRRAR GÅRDSHUSETS FASAD MOT ÖSTER. | |
| SKALA 1:100 | UPPDRAGSNUMMER A3:04 |

Inkom till Stockholms stadsbyggnadskontor - 2016-10-13, Dnr 2016-17088

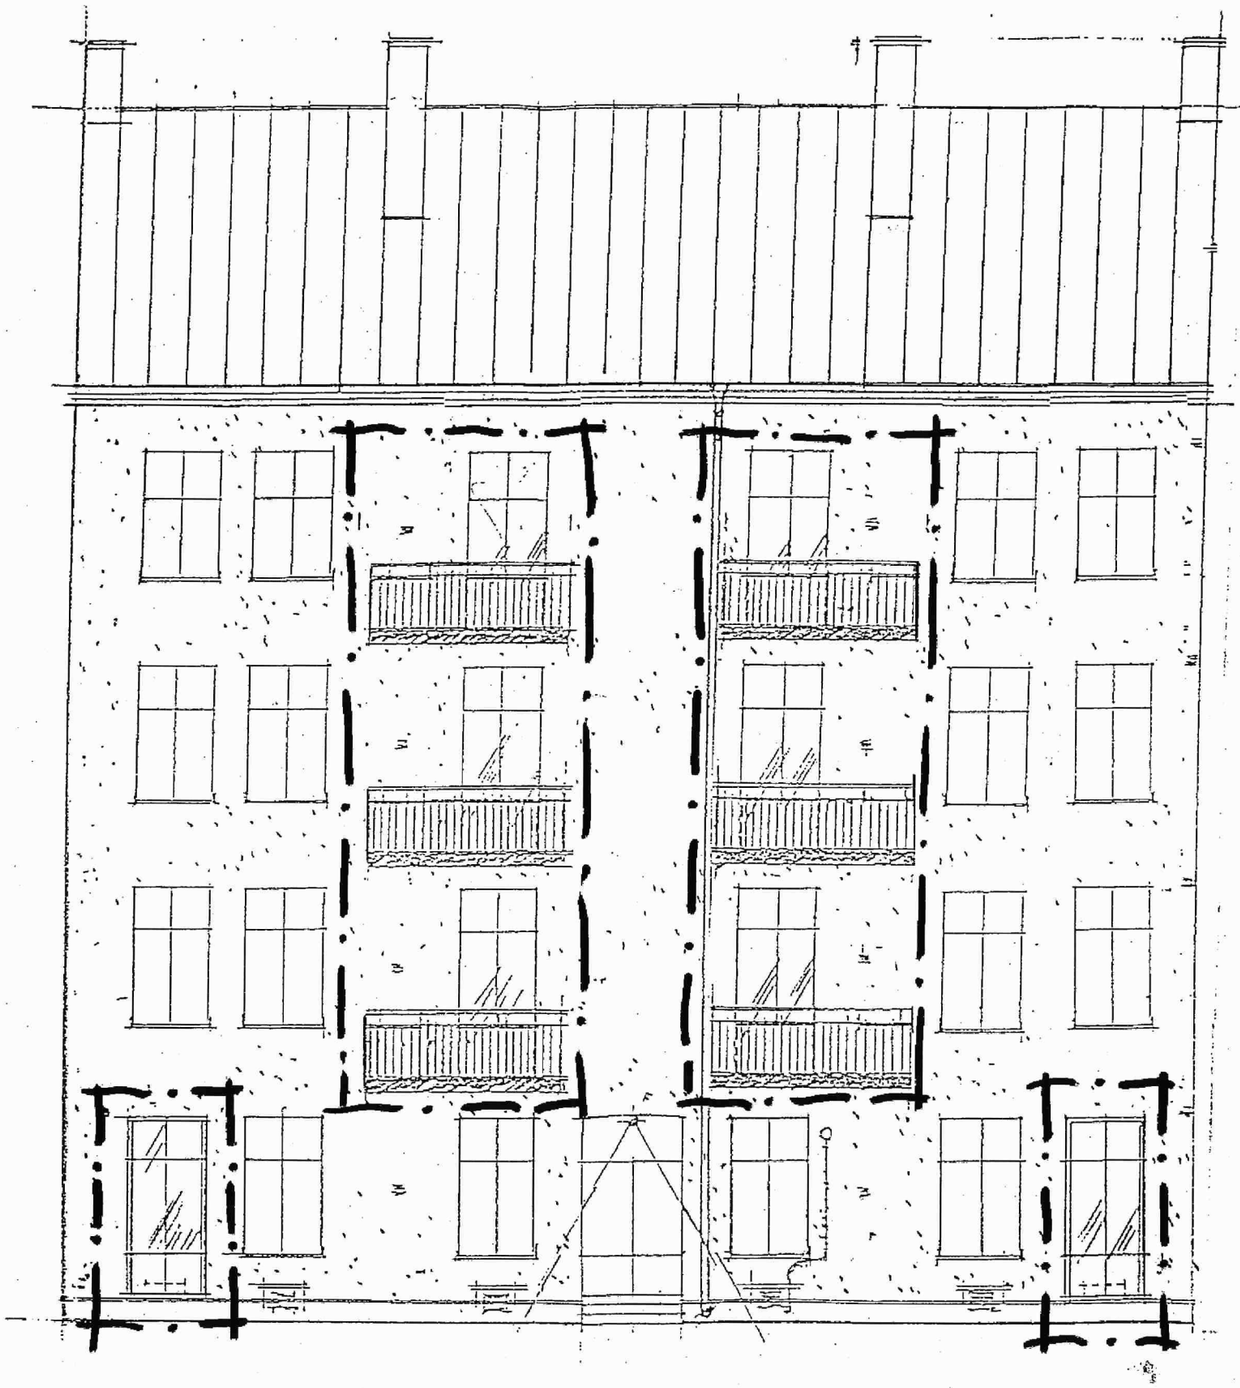

Ritning för tidigare beviljat lov för lägenheten gång 1

**ANMÄRKNINGAR**

*NYA BALKONGER OCH FÖNSTERDÖRRAR :*
*BALKONGUPPHÄNGNING MED DRAGSTAG .*
*RÄCKEN UTFÖRES SOM GALLERRÄCKE I SVART SMIDE.*
*DÖRRAR UTFÖRES SOM PARDÖRRAR LIKA BEF FÖNSTER.*
*ANTAL, PLANMÅTT OCH ~~PLACERING ENLIGT RITNING~~.*

STOCKHOLMS STAD Stadsbyggnadskontoret
Inkom Reg. 2016 -10- 13
Dnr. 16 - 17088 - 575

Granskad MK | STOCKHOLMS BYGGNADSNÄMND Tillhör nämndens beslut 2002-03-26

BYGGLOVETS OMFATTNING | SIGN. MK

STOCKHOLMS STAD Stadsbyggnads kontoret
Inkom Reg. 2002 -02- 28
Dnr. 01 - 14378 - 579

| | | | | |
|---|---|---|---|---|
| A | BALKONGER FLYTTADE | | MK | 020225 |
| REG. | ANT | REVIDERINGEN AVSER | SIGN | DATUM |

SKALA I MM
5 10 20 30 40 50 60 70 80 90 100


GTL KVALITETSANSVARIG ARKITEKT

ADRESS:
JÄRNEKSVÄGEN 4, 131 40 NACKA

EMAIL:

TELEFON : 08 - 556 152 53
MOBIL : 070 - 725 23 53
TELEFAX 08 - 556 152 54


ANSVARIG HANDLÄGGARE: GEORGE LEDDER
DATUM: 2001-08-31

# BYGGLOVSHANDLING


## *Kvarteret Vilan 17, Vasastaden*

*ÄNDRING AV GÅRDSFASADER MED BALKONGER & FÖNSTERDÖRRAR GÅRDSHUSETS FASAD MOT ÖSTER.*

| SKALA | RITNINGSNUMMER | ÄNDR.SET |
|---|---|---|
| 1 : 100 | A3:04 | A |

Inkom till Stockholms stadsbyggnadskontor - 2016-10-13, Dnr 2016-17088

Lämnas in i 2ex

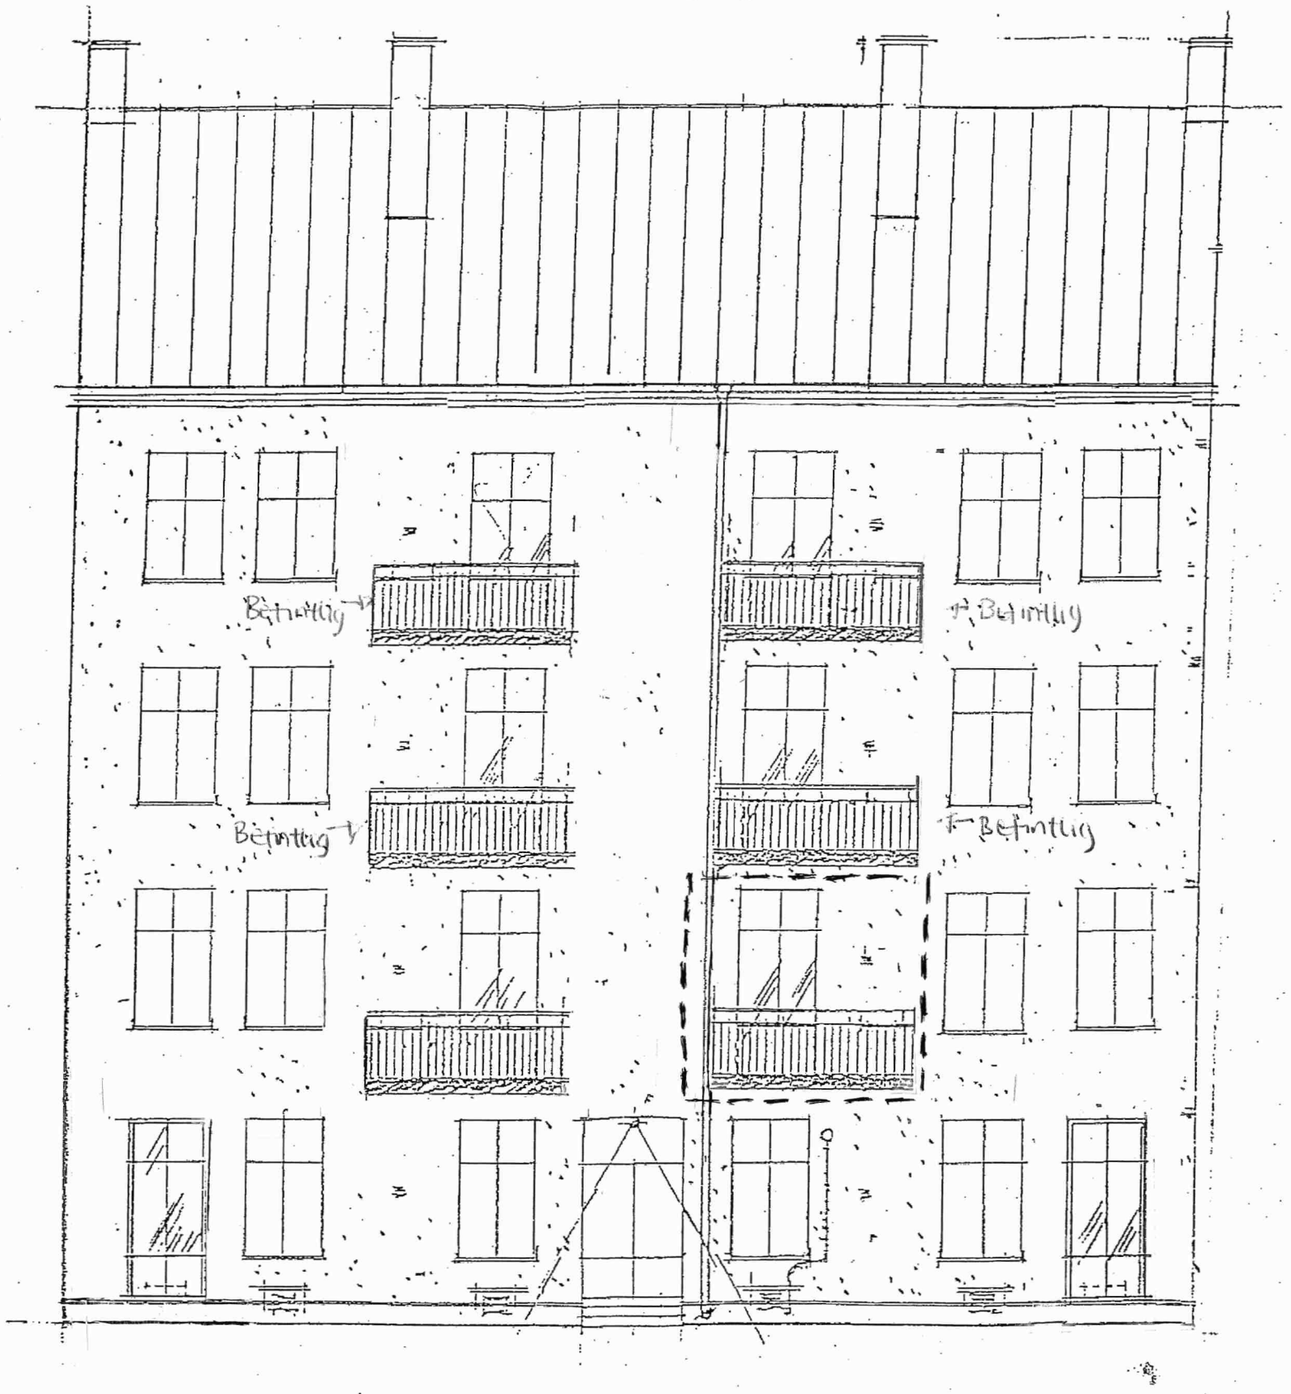


## ANMÄRKNINGAR

*NYA BALKONGER OCH FÖNSTERDÖRRAR :*
*BALKONGUPPHÄNGNING MED DRAGSTAG .*
*RÄCKEN UTFÖRES SOM GALLERRÄCKE I SVART SMIDE.*
*DÖRRAR UTFÖRES SOM PARDÖRRAR LIKA BEF FÖNSTER.*
*ANTAL, PLANMÅTT OCH PLACERING ENLIGT RITNING.*

Stadsbyggnadskontoret
Inkom 2016 -10- 13
Reg.
Dnr: 17088/575

Stadsbyggnads kontoret
Inkom
Reg.
Dnr.

| REG. | ANT | REVIDERINGEN AVSER | SIGN | DATUM |
|---|---|---|---|---|
| A | | BALKONGER FLYTTADE | | 020225 |

SKALA I MM
5 10 20 30 40 50 60 70 80 90 100

G T E KVALITETSANSVARIG ARKITEKT

ADRESS:
JÄRNEKSVÄGEN 4, 131 40 NACKA

EMAIL:

TELEFON : 08 - 556 152 53
MOBIL : 070 - 725 23 53
TELEFAX 08 - 556 152 54

ANSVARIG HANDLÄGGARE: GEORGE LEDDER
DATUM: 2001-08-31

# BYGGLOVSHANDLING

## *Kvarteret Vilan 17, Vasastaden*

*ÄNDRING AV GÅRDSFASADER MED BALKONGER & FÖNSTERDÖRRAR GÅRDSHUSETS FASAD MOT ÖSTER.*

| SKALA | RITNINGSNUMMER | ÄNDR SET |
|---|---|---|
| 1 : 100 | A3:04 | A |

Inkom till Stockholms stadsbyggnadskontor - 2016-10-13, Dnr 2016-17088