
Inkom till Stockholms stadsbyggnadskontor - 2019-03-29, Dnr 2019-02459

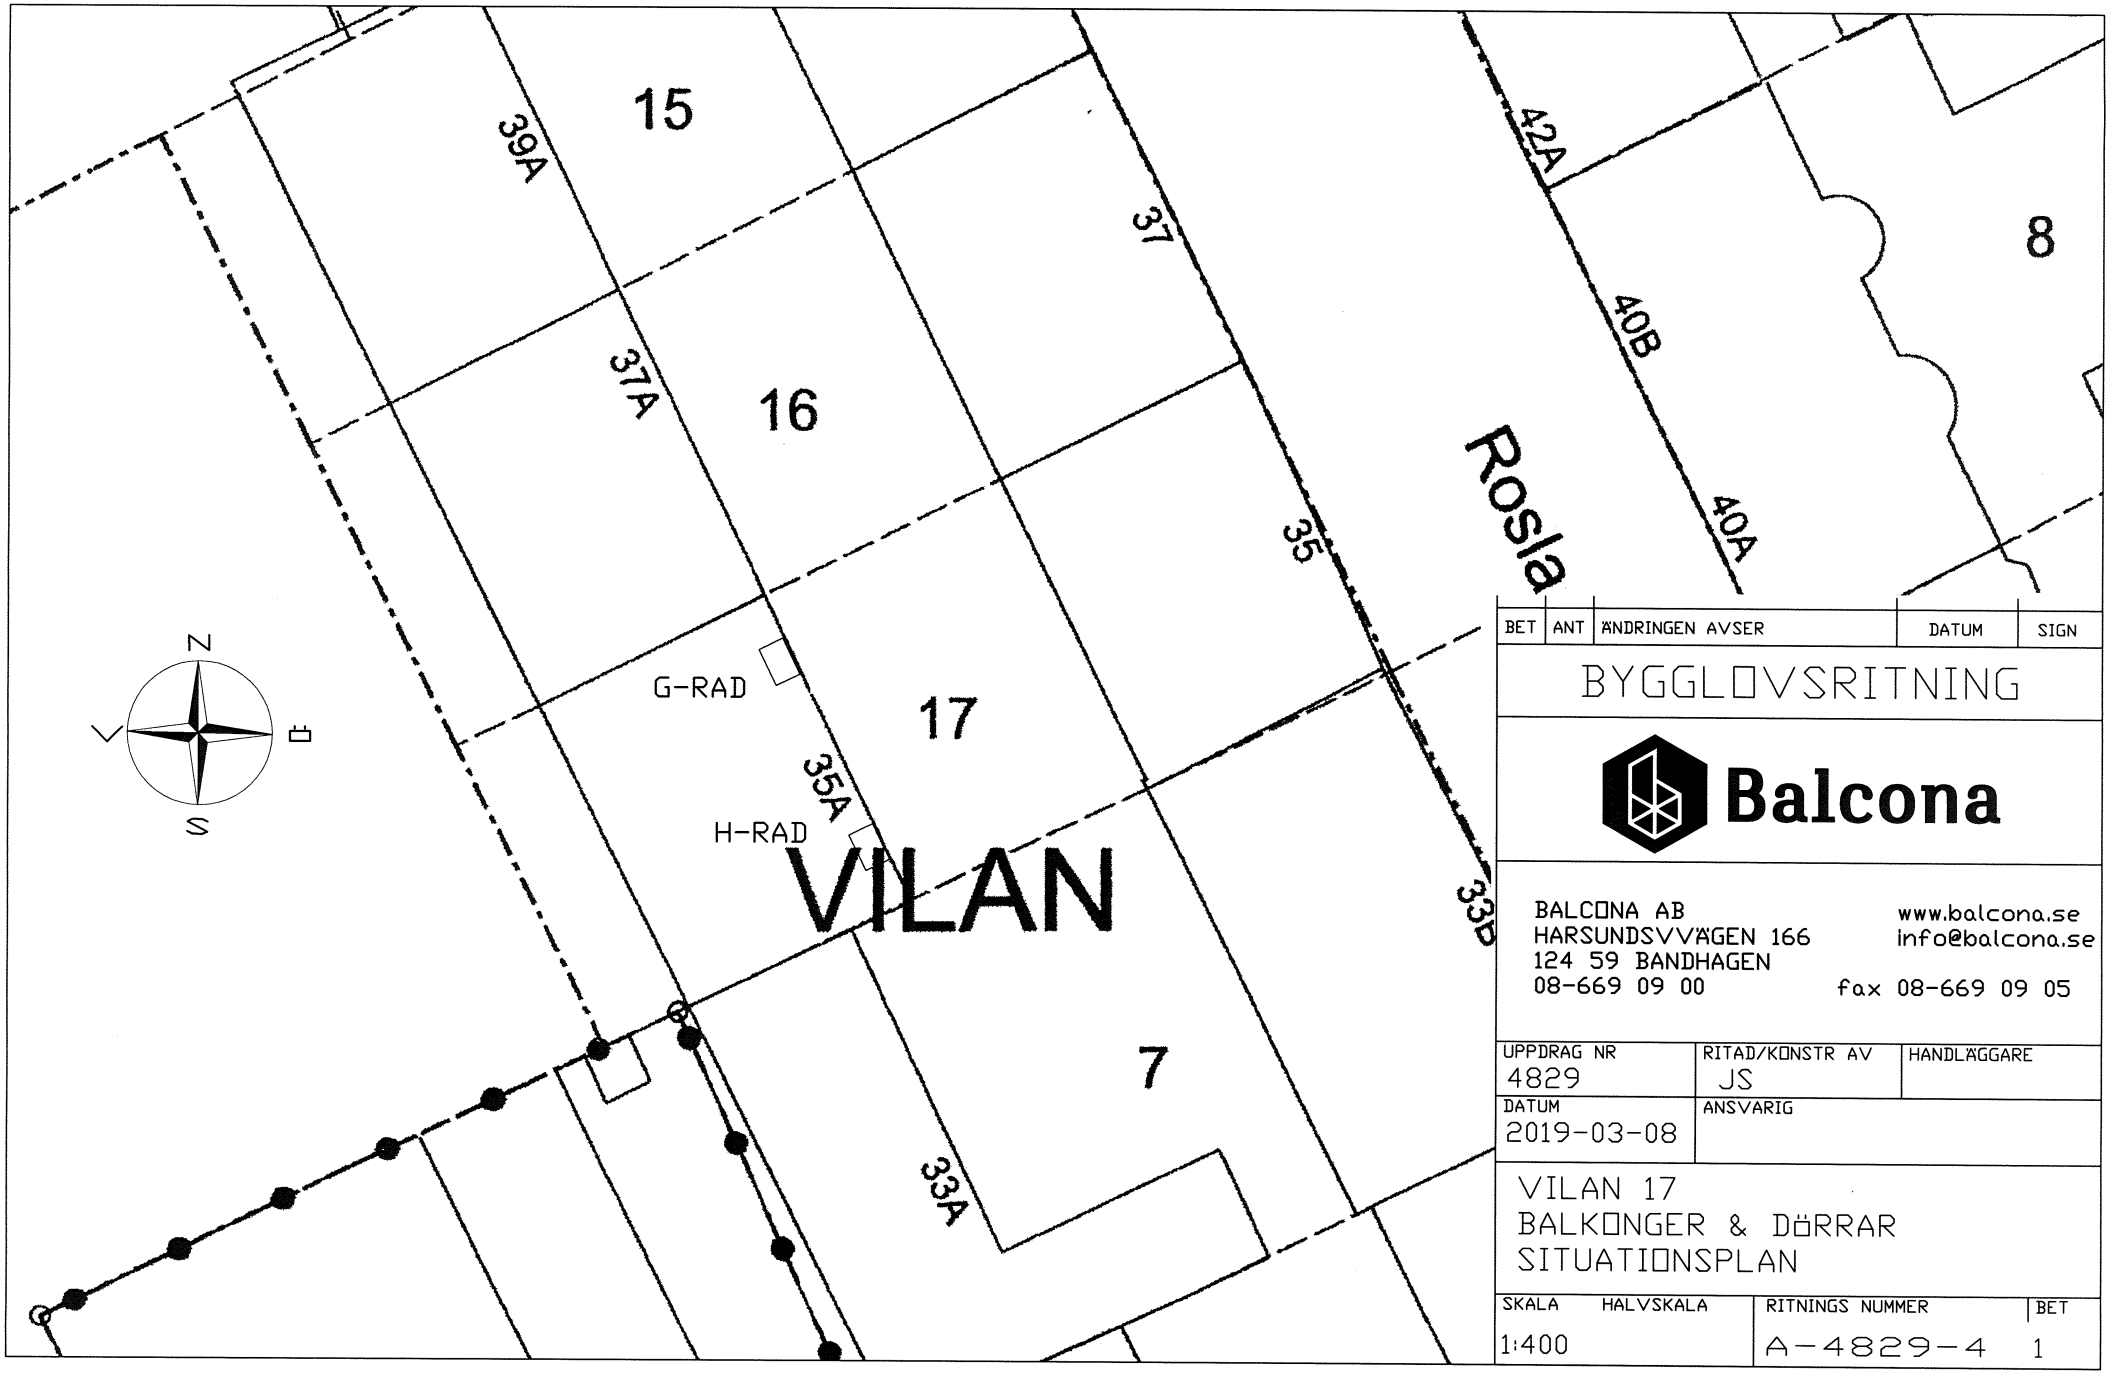

BET	ANT	ÄNDRINGEN AVSER	DATUM	SIGN

BYGGLOVSRITNING


Balcona

BALCONA AB
HARSUNDSVVÄGEN 166
124 59 BANDHAGEN
08-669 09 00
www.balcona.se
info@balcona.se
fax 08-669 09 05

UPPDRAG NR	RITAD/KONSTR AV	HANDLÄGGARE
4829	JS	
DATUM	ANSVARIG	
2019-03-08		

VILAN 17
BALKONGER & DÖRRAR
SITUATIONSPLAN

SKALA HALVSKALA	RITNINGS NUMMER	BET
1:400	A-4829-4	1

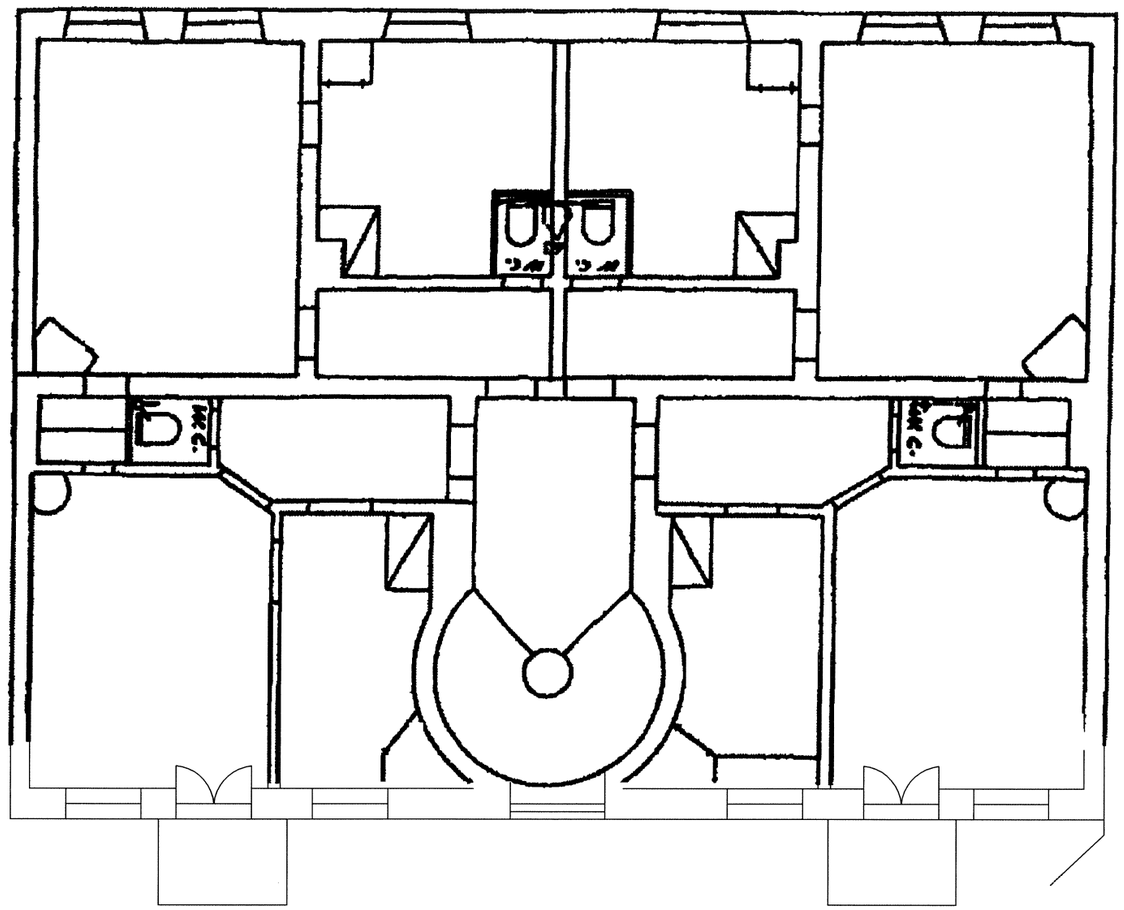

ANVISNINGAR

BEFINTLIG KARM RIVES OCH DEN NYA KARMEN MONTERAS I DESS STÄLLE. BALKONGPLATTANS UNDERSIDA UTFÖRES SLÄT. PINNRÄCKE AV SMIDESSTÅL I KULÖR SVART. INFÄSTNING ENLIGT K-RITNING.

I DE POSITIONER DÄR BRANDUTRYMNING ÖNSKAS, MONTERAS BALKONG MED INTEGRERAD BRANDUTRYMNING (STEGE + LUCKA).

G-RAD
ca 2100 x 1400
BEF FD I BV PLAN 0
ENLIGT TIDIGARE BEVILJAT LOV
DNR: 2009-22338-571

EJ UTFÖRDA BALKONGER PLAN 2
BEVILJADE ENLIGT
DNR: 2009-22338-571

H-RAD
ca 2100 x 1400
BEF FRANSKA DÖRRAR PLAN 1, 4
BEF FD I BV PLAN 0
ENLIGT TIDIGARE BEVILJAT LOV
DNR: 2009-22338-571

EJ UTFÖRDA BALKONGER PLAN 2
BEVILJADE ENLIGT
DNR: 2009-22338-571

NORMALPLAN skala 1:100

BET	ANT	ÄNDRINGEN AVSER	DATUM	SIGN

BYGGLOVSRITNING

Balcona


BALCONA AB
HARSUNDSVVÄGEN 166
124 59 BANDHAGEN
08-669 09 00
www.balcona.se
info@balcona.se
fax 08-669 09 05

UPPDRAG NR	RITAD/KONSTR AV	HANDLÄGGARE
4829	JS	
DATUM	ANSVARIG	
2019-03-08		

VILAN 17
BALKONGER & DÖRRAR
NORMALPLAN

SKALA HALVSKALA	RITNINGS NUMMER	BET
1:100	A-4829-1	1

Inkom till Stockholms stadsbyggnadskontor - 2019-03-29, Dnr 2019-02459

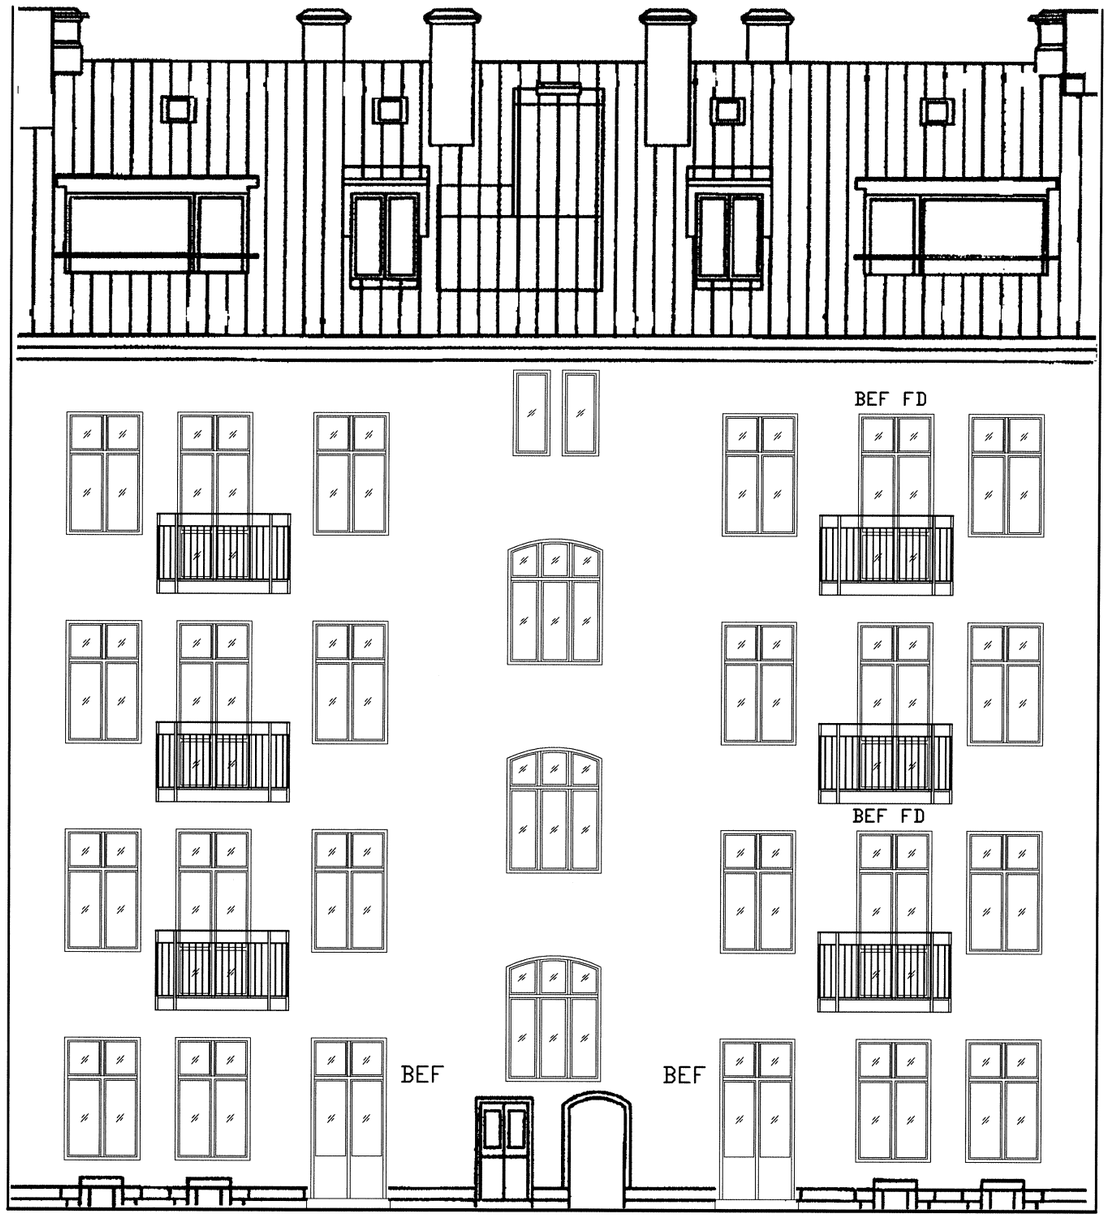

FASAD MOT VÄST skala 1:100

ANVISNINGAR

BEFINTLIG KARM RIVES OCH DEN NYA KARMEN MONTERAS I DESS STÄLLE. BALKONGPLATTANS UNDERSIDA UTFÖRES SLÄT. PINNRÄCKE AV SMIDESSTÅL I KULÖR SVART. INFÄSTNING ENLIGT K-RITNING.

I DE POSITIONER DÄR BRANDUTRYMNING ÖNSKAS, MONTERAS BALKONG MED INTEGRERAD BRANDUTRYMNING (STEGE + LUCKA).

BET	ANT	ÄNDRINGEN AVSER	DATUM	SIGN

BYGGLOVSRITNING

Balcona


BALCONA AB
HARSUNDSVVÄGEN 166
124 59 BANDHAGEN
08-669 09 00
www.balcona.se
info@balcona.se
fax 08-669 09 05


UPPDRAG NR	RITAD/KONSTR AV	HANDLÄGGARE
4829	JS	
DATUM	ANSVARIG	
2019-03-08		

VILAN 17
BALKONGER & DÖRRAR
FASAD MOT VÄST


SKALA	HALVSKALA	RITNINGS NUMMER	BET
1:100		A-4829-2	1

Inkom till Stockholms stadsbyggnadskontor - 2019-03-29, Dnr 2019-02459

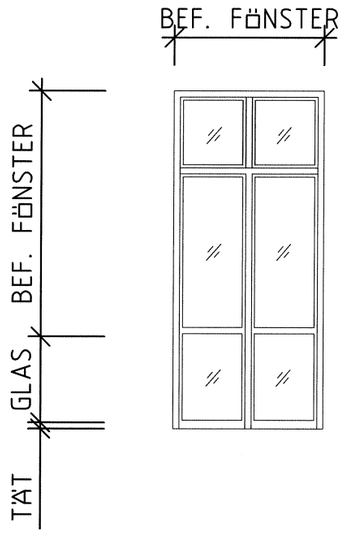

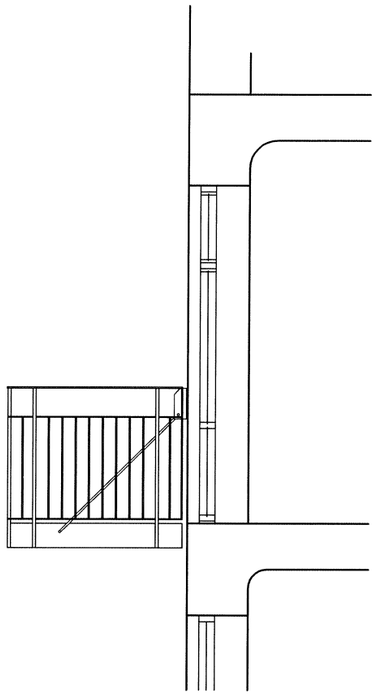

BALKONGDÖRR skala 1:50

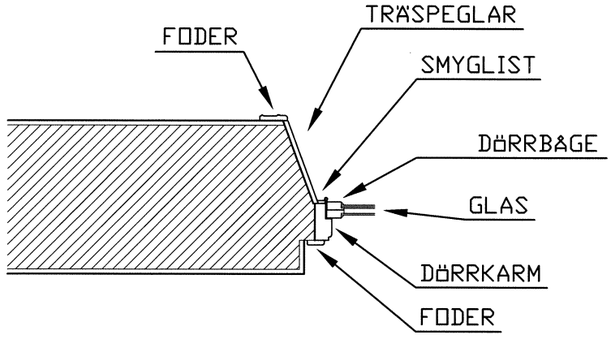

TVÄRSNITT VÄGG / BALKONGDÖRR skala 1:20

ANVISNINGAR

BEFINTLIG KARM RIVES OCH DEN NYA KARMEN MONTERAS I DESS STÄLLE. BALKONGPLATTANS UNDERSIDA UTFÖRES SLÄT. PINNRÄCKE AV SMIDESSTÅL I KULÖR SVART. INFÄSTNING ENLIGT K-RITNING.

I DE POSITIONER DÄR BRANDUTRYMNING ÖNSKAS, MONTERAS BALKONG MED INTEGRERAD BRANDUTRYMNING (STEGE + LUCKA).

BET	ANT	ÄNDRINGEN AVSER	DATUM	SIGN

BYGGLOVSRITNING

Balcona

BALCONA AB
HARSUNDSVÄGEN 166
124 59 BANDHAGEN
08-669 09 00
www.balcona.se
info@balcona.se
fax 08-669 09 05

UPPDRAG NR	RITAD/KONSTR AV	HANDLÄGGARE
4829	JS	
DATUM	ANSVARIG	
2019-02-12		

VILAN 17
BALKONGER & DÖRRAR
DETALJ

SKALA	HALVSKALA	RITNINGS NUMMER	BET
1:50		A-4829-3	

Inkom till Stockholms stadsbyggnadskontor - 2019-03-29, Dnr 2019-02459