
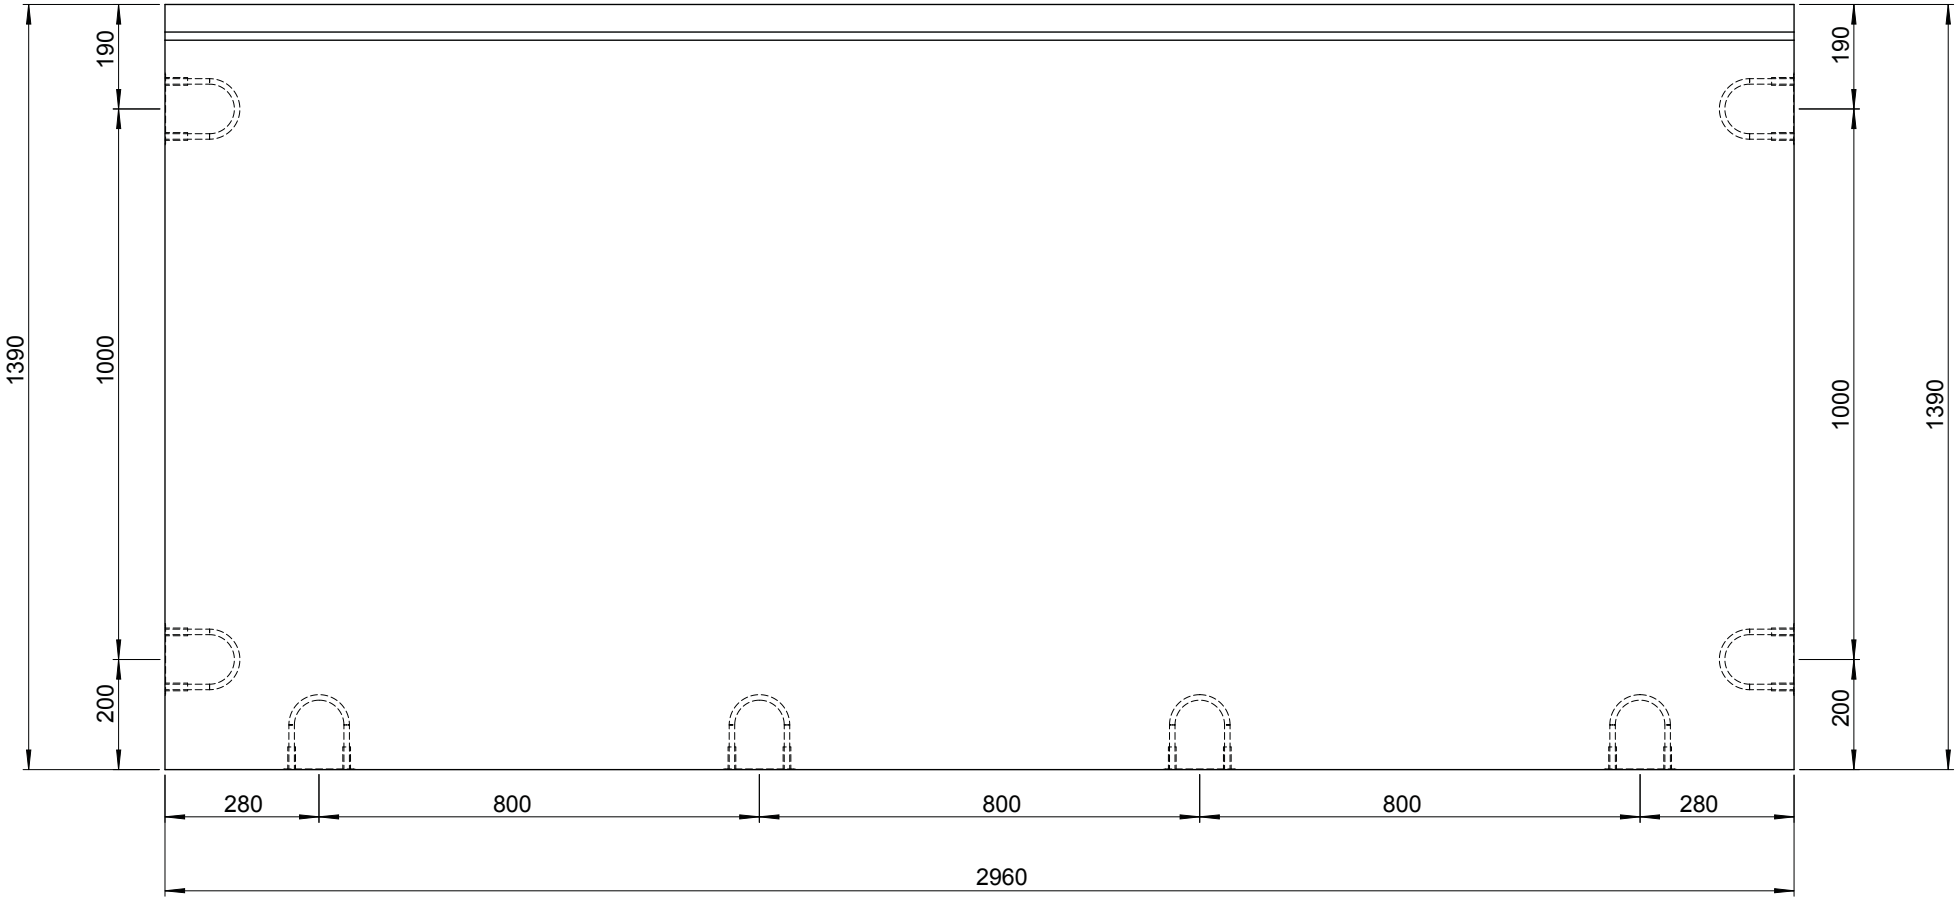


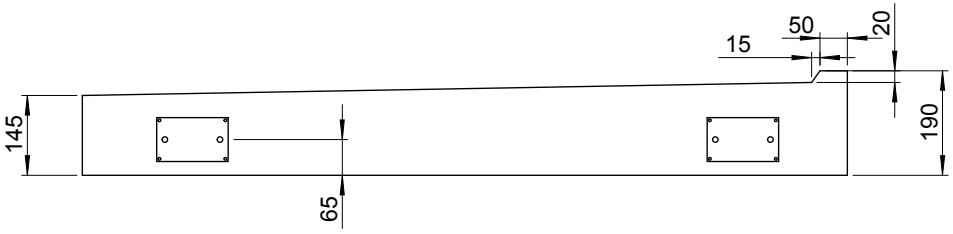

Inkom till Stockholms stadsbyggnadskontor - 2017-10-11, Dnr 2016-17088

Ritad av	Kontrollerad av	Tolerans		Filnamn	Datum	Skala
MP		SMS 715 medel			2017-08-10	1:10

SYSTEMBALKONG AB
BALKONGER • RÄCKEN • MONTAGE
BOX 19 770 70 Långshyttan
Tel: 0225-615 40. Fax: 61405

Titel/namn

Förslag placering ingjutningsgods btg-blk

Antal: 1st. Vikt:

Ritnings namn	Edition	Sheet
P29601390		1/1