
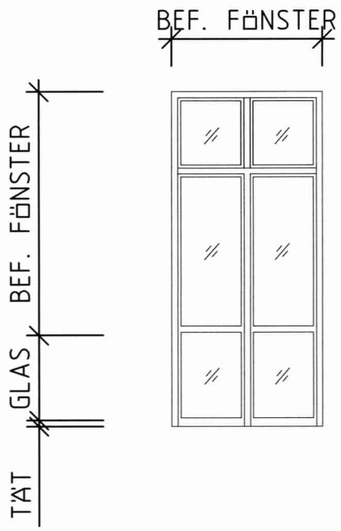


BALKONGDÖRR skala 1:50

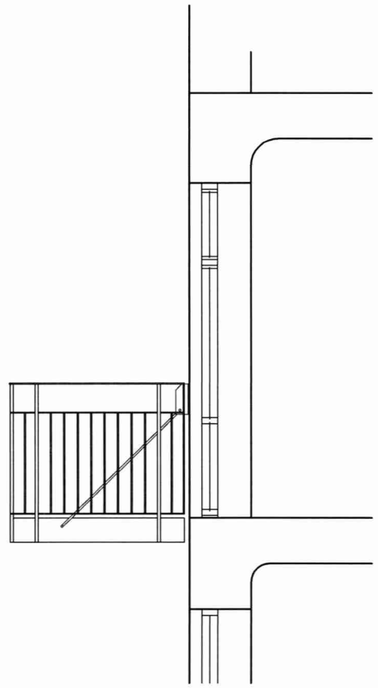


ANVISNINGAR

BEFINTLIG KARM RIVES OCH DEN NYA KARMEN MONTERAS I DESS STÄLLE. BALKONGPLATTANS UNDERSIDA UTFÖRES SLÄT. PINNRÄCKE AV SMIDESSTÅL I KULÖR SVART. INFÄSTNING ENLIGT K-RITNING.

I DE POSITIONER DÄR BRANDUTRYMNING ÖNSKAS, MONTERAS BALKONG MED INTEGRERAD BRANDUTRYMNING (STEGE + LUCKA).

Stadsbyggnadskontoret
Inkom 2019 -02- 15
Reg.
Dnr: 19-02459-575

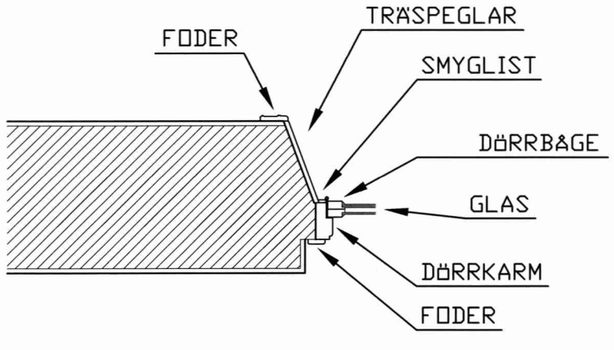

TVÄRSNITT VÄGG / BALKONGDÖRR skala 1:20

BET	ANT	ÄNDRINGEN AVSER	DATUM	SIGN

BYGGLOVSRITNING

Balcona

BALCONA AB
HARSUNDSVVÄGEN 166
124 59 BANDHAGEN
08-669 09 00
www.balcona.se
info@balcona.se
fax 08-669 09 05

UPPDRAG NR	RITAD/KONSTR AV	HANDLÄGGARE
4829	JS	
DATUM	ANSVARIG	
2019-02-12		

VILAN 17
BALKONGER & DÖRRAR
DETALJ

SKALA HALVSKALA	RITNINGS NUMMER	BET
1:50	A-4829-3	

Inkom till Stockholms stadsbyggnadskontor - 2019-02-15, Dnr 2019-02459