

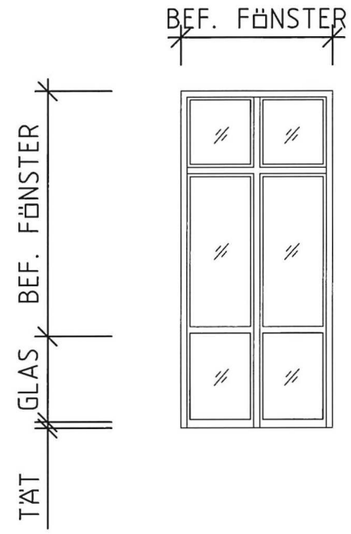


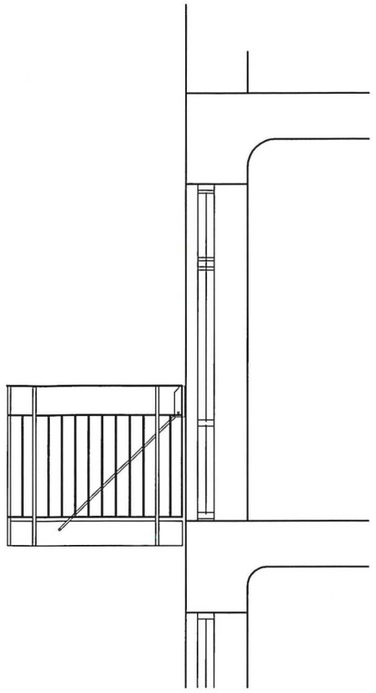

BALKONGDÖRR skala 1:50

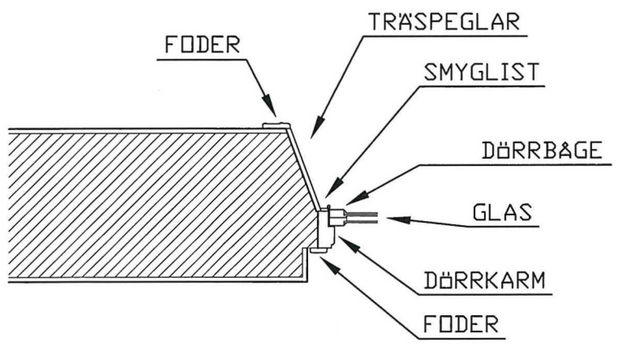

TVÄRSNITT VÄGG / BALKONGDÖRR skala 1:20

ANVISNINGAR

BEFINTLIG KARM RIVES OCH DEN NYA KARMEN MONTERAS I DESS STÄLLE. BALKONGPLATTANS UNDERSIDA UTFÖRES SLÄT. PINNRÄCKE AV SMIDESSTÅL I KULÖR SVART.

INFÄSTNING ENLIGT K-RITNING.

ANSÖKAN AVSER BALKONG OCH FÖNSTERDÖRR G1

TIDIGARE BEVILJAT LOV
DNR: 2019-02459-575

Stadsbyggnadskontoret
Inkom Reg. 2024 -12- 03
Dnr: 2024-18303

BET	ANT	ÄNDRINGEN AVSER	DATUM	SIGN

BYGGLOVSRITNING

Balcona

BALCONA AB
SOCKENVÄGEN 477
122 33 ENSKEDE
08-669 09 00
www.balcona.se
offert@balcona.se

UPPDRAG NR	RITAD/KONSTR AV	HANDLÄGGARE
5367	JS	
DATUM	ANSVARIG	
2024-11-01		

VILAN 17
BALKONG & DÖRR
DETALJ

SKALA HALVSKALA	RITNINGS NUMMER	BET
1:50	A-5367-D1	

Inkom till Stockholms stadsbyggnadskontor - 2024-12-03, Dnr 2024-18303