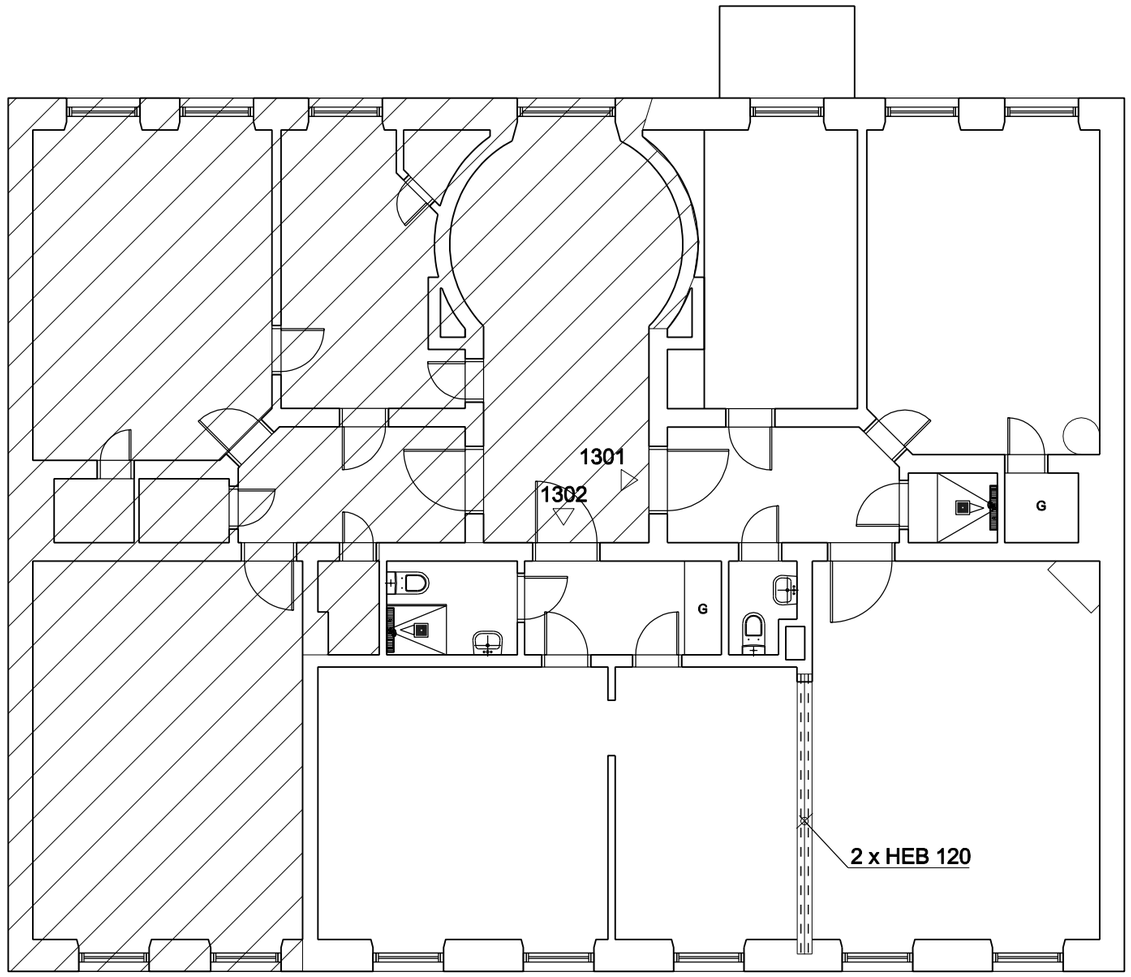


PLAN BEF SKALA 1:100

SKALA 1:100 1m 0 2,5 5m

BET	ANT	ÄNDRINGEN AVSER	DATUM	SIGN

BYGGLOVSRITNING

FASTIGHET OCH PROJEKTNAMN
SAMMANSLAGNING AV LÄGENHET 1301 &1302
ROSLAGSGATAN 35, GATUHUSET

A Aleksandar Carapic — Tel: 073-634 34 76
Civilingenjör/Konstruktör
Erikas väg 14, 153 38 Järna
aleksandar.carapic@gmail.com

RITAD/KONSTR AV: Aleksandar Carapic

DATUM: 2026-02-10 | ANSVARIG: Aleksandar Carapic

RITNINGENS INNEHÅLL

AVVÄXLING
PLAN BEF

SKALA	RITNINGSNR	BET
1:100/A3	A-30-03	

Inkom till Stockholms stadsbyggnadskontor - 2026-02-12, Dnr 2026-02453