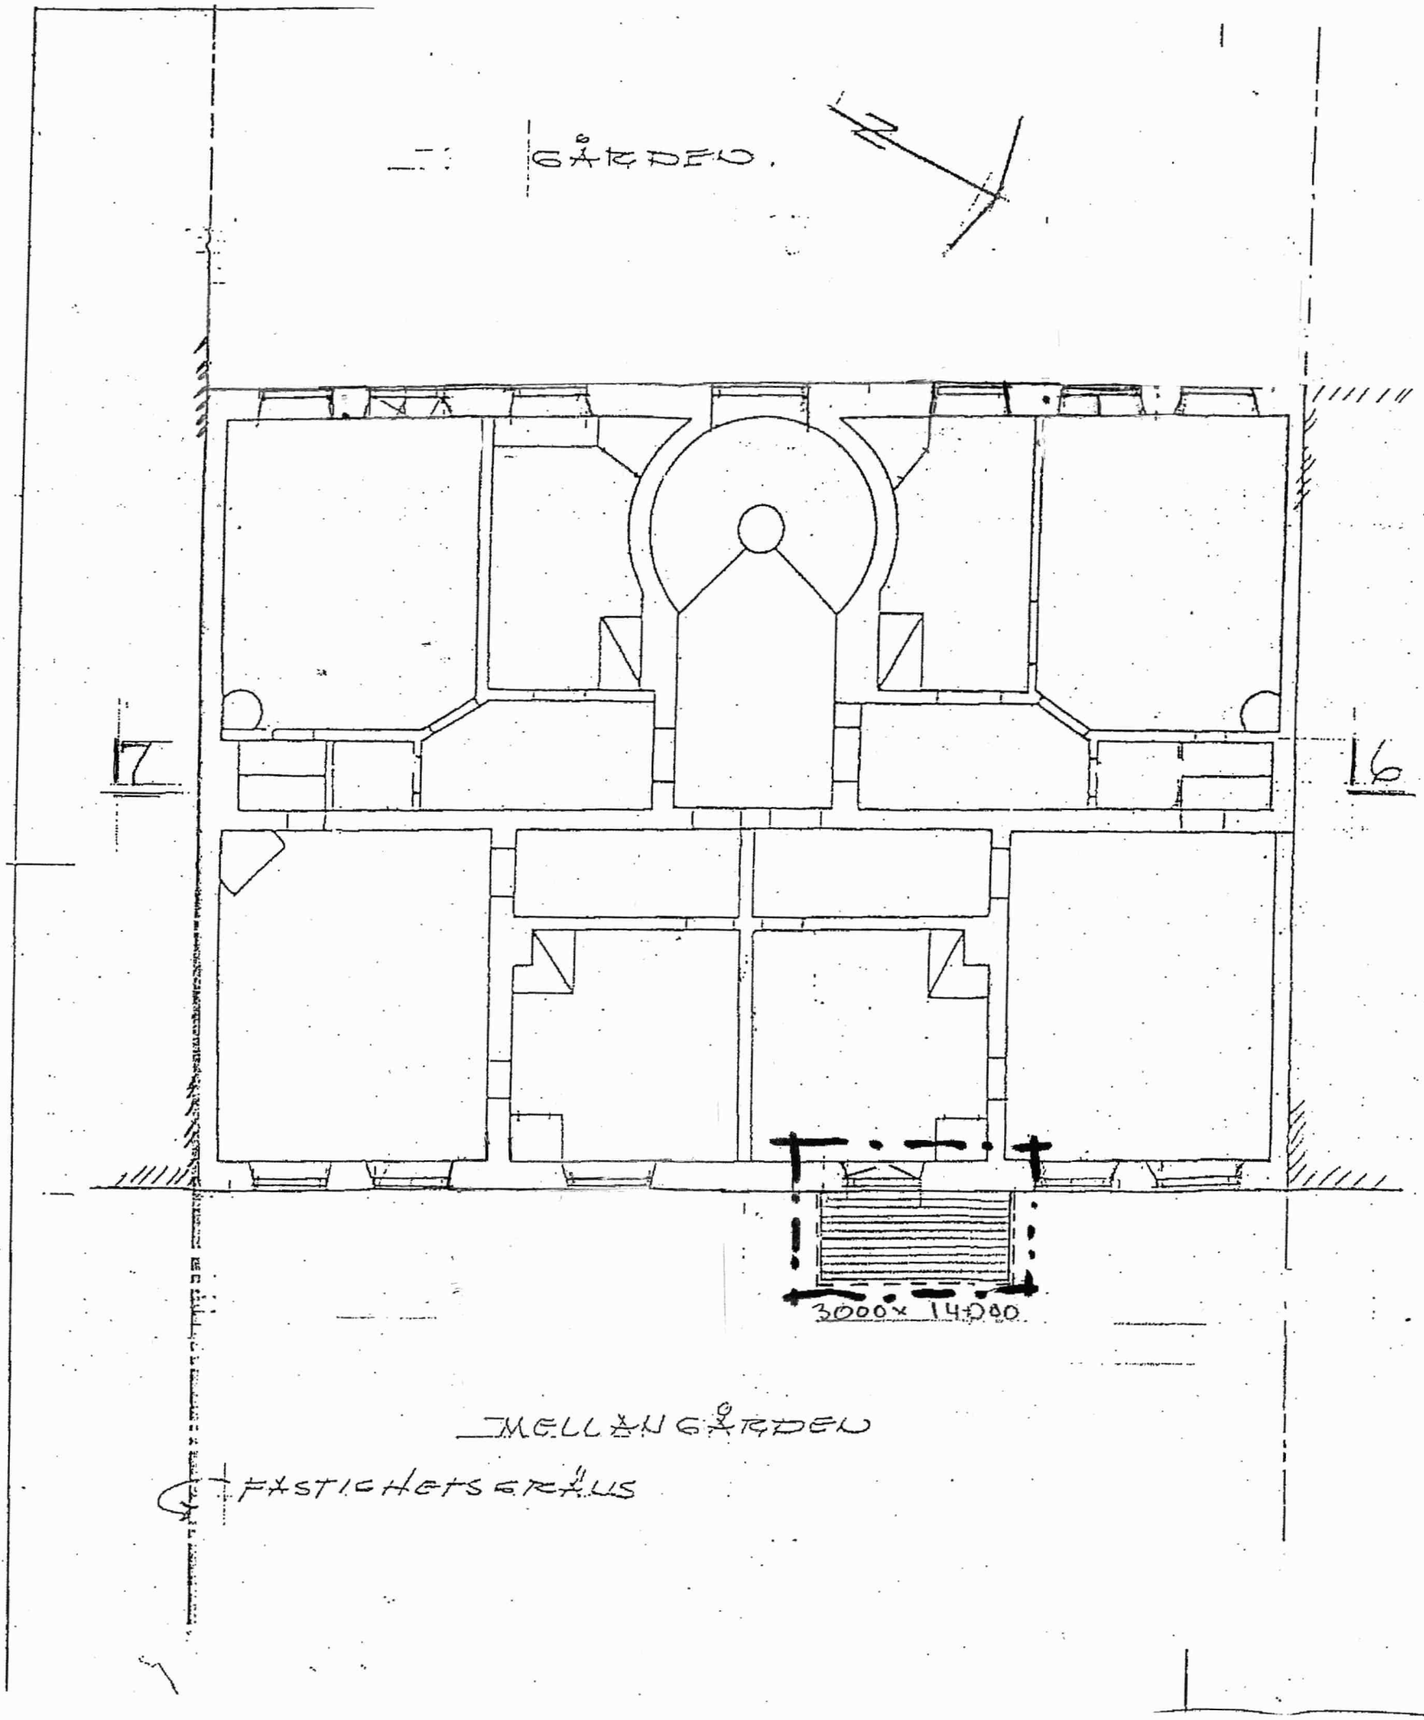


ANMÄRKNINGAR

NYA BALKONGER OCH FÖNSTERDÖRRAR:
BALKONGUPPHÄNGNING MED DRAGSTAG.
RÄCKEN UTFÖRES SOM GALLERRÄCKE I SVART SMIDE.
DÖRRAR UTFÖRES SOM PARDÖRRAR LIKA BEF FÖNSTER
ANTAL, PLANMÅTT OCH PLACERING ENLIGT RITNING.

Stadsbyggnadskontoret
Inkom 2016 -10- 13
Reg.
Dnr. 16-17088-57

Stadsbyggnads kontoret
Inkom
Reg.
Dnr.

B		BALKONGER PLACER. & STORLEK	SB	020222
A		BALKONGER MOT BAKGÅRD UTGÅR	SB	011221
ÄG.	ÄND	ÄNDRINGENS ART	SIGN	DATUM

SKALA i MM
5 | 10 | 20 | 30 | 40 | 50 | 60 | 70 | 80 | 90 | 100

G T L KVALITETSANSVARIG ARKITEKT

ADRESS
JÄRNEKSVÄGEN 4, 131 40 NACKA

E-MAIL:

TELEFON 1: 08 - 556 152 53
MOBIL: 070 - 725 23 53
TELEFAX: 08 - 556 152 54

ANSVARIG HANDLÄGGARE: GEORGE LEDDER
DATUM: 2001-08-31

BYGGLOVSHANDLING

Kvarteret Vilan 17, Vasastaden

ÄNDRING AV GÅRDSFASADER MED BALKONGER & FÖNSTERDÖRRAR: GÅRDSHUSETS VÅNINGSPLAN 1 - 3TR.

SKALA	RITNINGSNUMMER	ÄNDR BET
1:100	A3:03	B.

Inkom till Stockholms stadsbyggnadskontor - 2016-10-13, Dnr 2016-17088