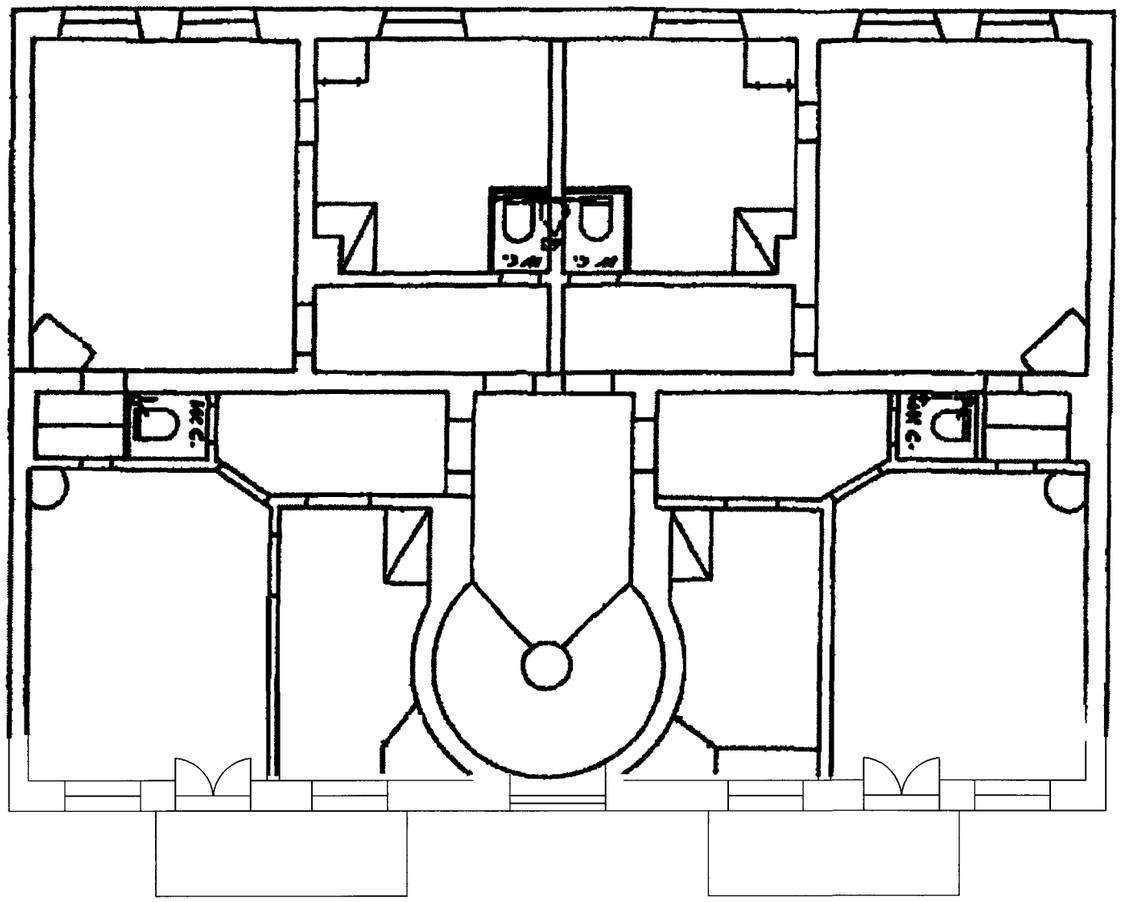

ANVISNINGAR

BEFINTLIG KARM RIVES OCH DEN NYA KARMEN MONTERAS I DESS STÄLLE. BALKONGPLATTANS UNDERSIDA UTFÖRES SLÄT. PINNRÄCKE AV SMIDESSTÅL I KULÖR SVART. INFÄSTNING ENLIGT K-RITNING.

I DE POSITIONER DÄR BRANDUTRYMNING ÖNSKAS, MONTERAS BALKONG MED INTEGRERAD BRANDUTRYMNING (STEGE + LUCKA).

Stadsbyggnadskontoret
Inkom 2019 -02- 15
Reg.
Dnr: 02459-57

G-RAD
4100 x 1400
BEF FD I BV PLAN 0
ENLIGT TIDIGARE BEVILJAT LOV
DNR: 2009-22338-571

EJ UTFÖRDA BALKONGER PLAN 2
BEVILJADE ENLIGT
DNR: 2009-22338-571

H-RAD
4100 x 1400
BEF FRANSKA DÖRRAR PLAN 1, 4
BEF FD I BV PLAN 0
ENLIGT TIDIGARE BEVILJAT LOV
DNR: 2009-22338-571

EJ UTFÖRDA BALKONGER PLAN 2
BEVILJADE ENLIGT
DNR: 2009-22338-571

NORMALPLAN skala 1:100

BET	ANT	ÄNDRINGEN AVSER	DATUM	SIGN

BYGGLOVSRITNING

Balcona

BALCONA AB
HARSUNDSVÄGEN 166
124 59 BANDHAGEN
08-669 09 00
www.balcona.se
info@balcona.se
fax 08-669 09 05

UPPDRAG NR	RITAD/KONSTR AV	HANDLÄGGARE
4829	JS	
DATUM	ANSVARIG	
2019-02-12		

VILAN 17
BALKONGER & DÖRRAR
NORMALPLAN

SKALA HALVSKALA	RITNINGS NUMMER	BET
1:100	A-4829-1	

Inkom till Stockholms stadsbyggnadskontor - 2019-02-15, Dnr 2019-02459