
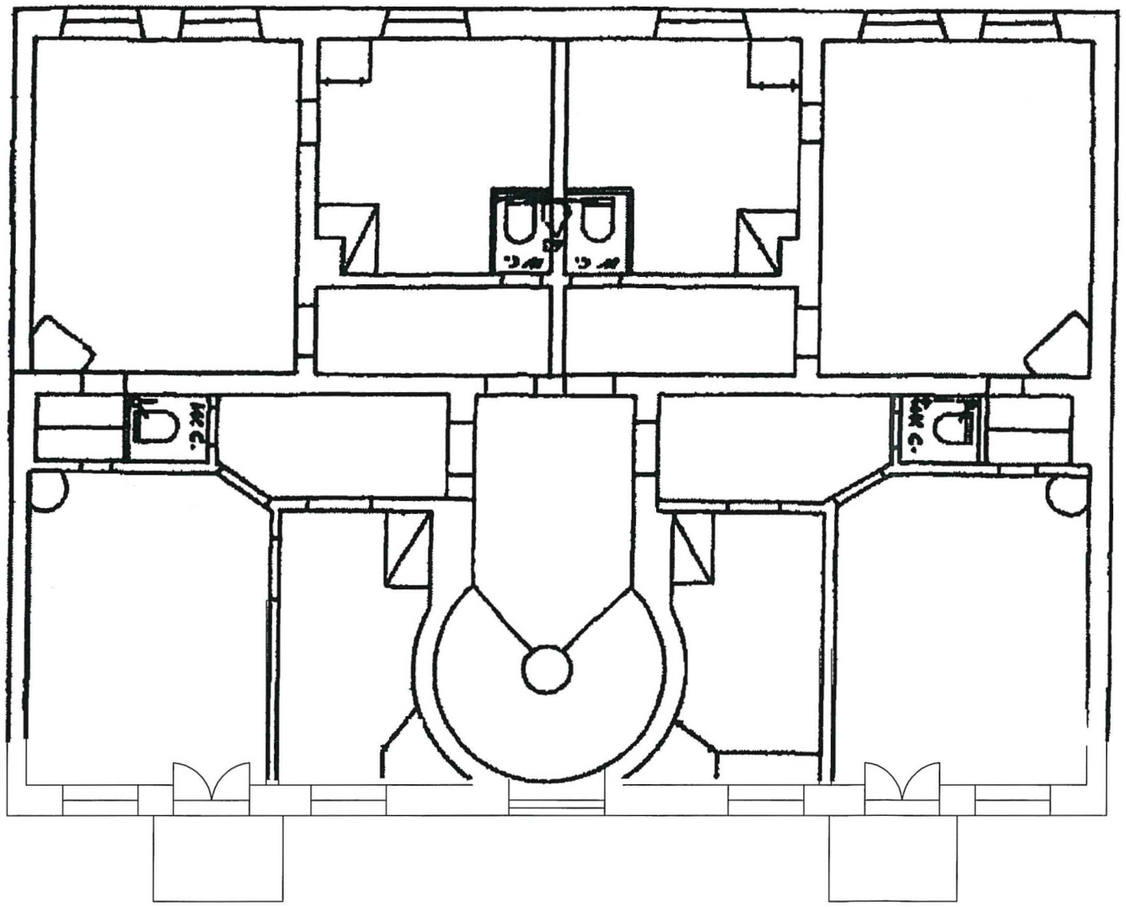


G-RAD
2100 x 1400
BEF PLAN 3

TILLKOMMANDE FÖNSTERDÖRR
OCH BALKONG G1

H-RAD
2100 x 1400
BEF PLAN 1, 2, 3

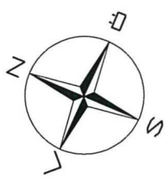

PLAN GÅRDSHUS
skala 1:100

0 1 2 3 4 5 10M

ANVISNINGAR

BEFINTLIG KARM RIVES OCH DEN NYA KARMEN MONTERAS I DESS STÄLLE. BALKONGPLATTANS UNDERSIDA UTFÖRES SLÄT. PINNRÄCKE AV SMIDESSTÅL I KULÖR SVART.

INFÄSTNING ENLIGT K-RITNING.

ANSÖKAN AVSER BALKONG OCH FÖNSTERDÖRR G1

TIDIGARE BEVILJAT LOV
DNR: 2019-02459-575

STOCKHOLMS STAD Stadsbyggnadskontoret
Inkom 2024 -12- 03
Reg.
Dnr: 2024-18303

BET	ANT	ÄNDRINGEN AVSER	DATUM	SIGN

BYGGLOVSRITNING

Balcona

BALCONA AB
SOCKENVÄGEN 477
122 33 ENSKEDE
08-669 09 00
www.balcona.se
offert@balcona.se

UPPDRAG NR	RITAD/KONSTR AV	HANDLÄGGARE
5367	JS	
DATUM	ANSVARIG	
2024-11-01		

VILAN 17
BALKONG & DÖRR
PLAN GÅRDSHUS

SKALA HALVSKALA	RITNINGS NUMMER	BET
1:100	A-5367-P1	

Inkom till Stockholms stadsbyggnadskontor - 2024-12-03, Dnr 2024-18303